


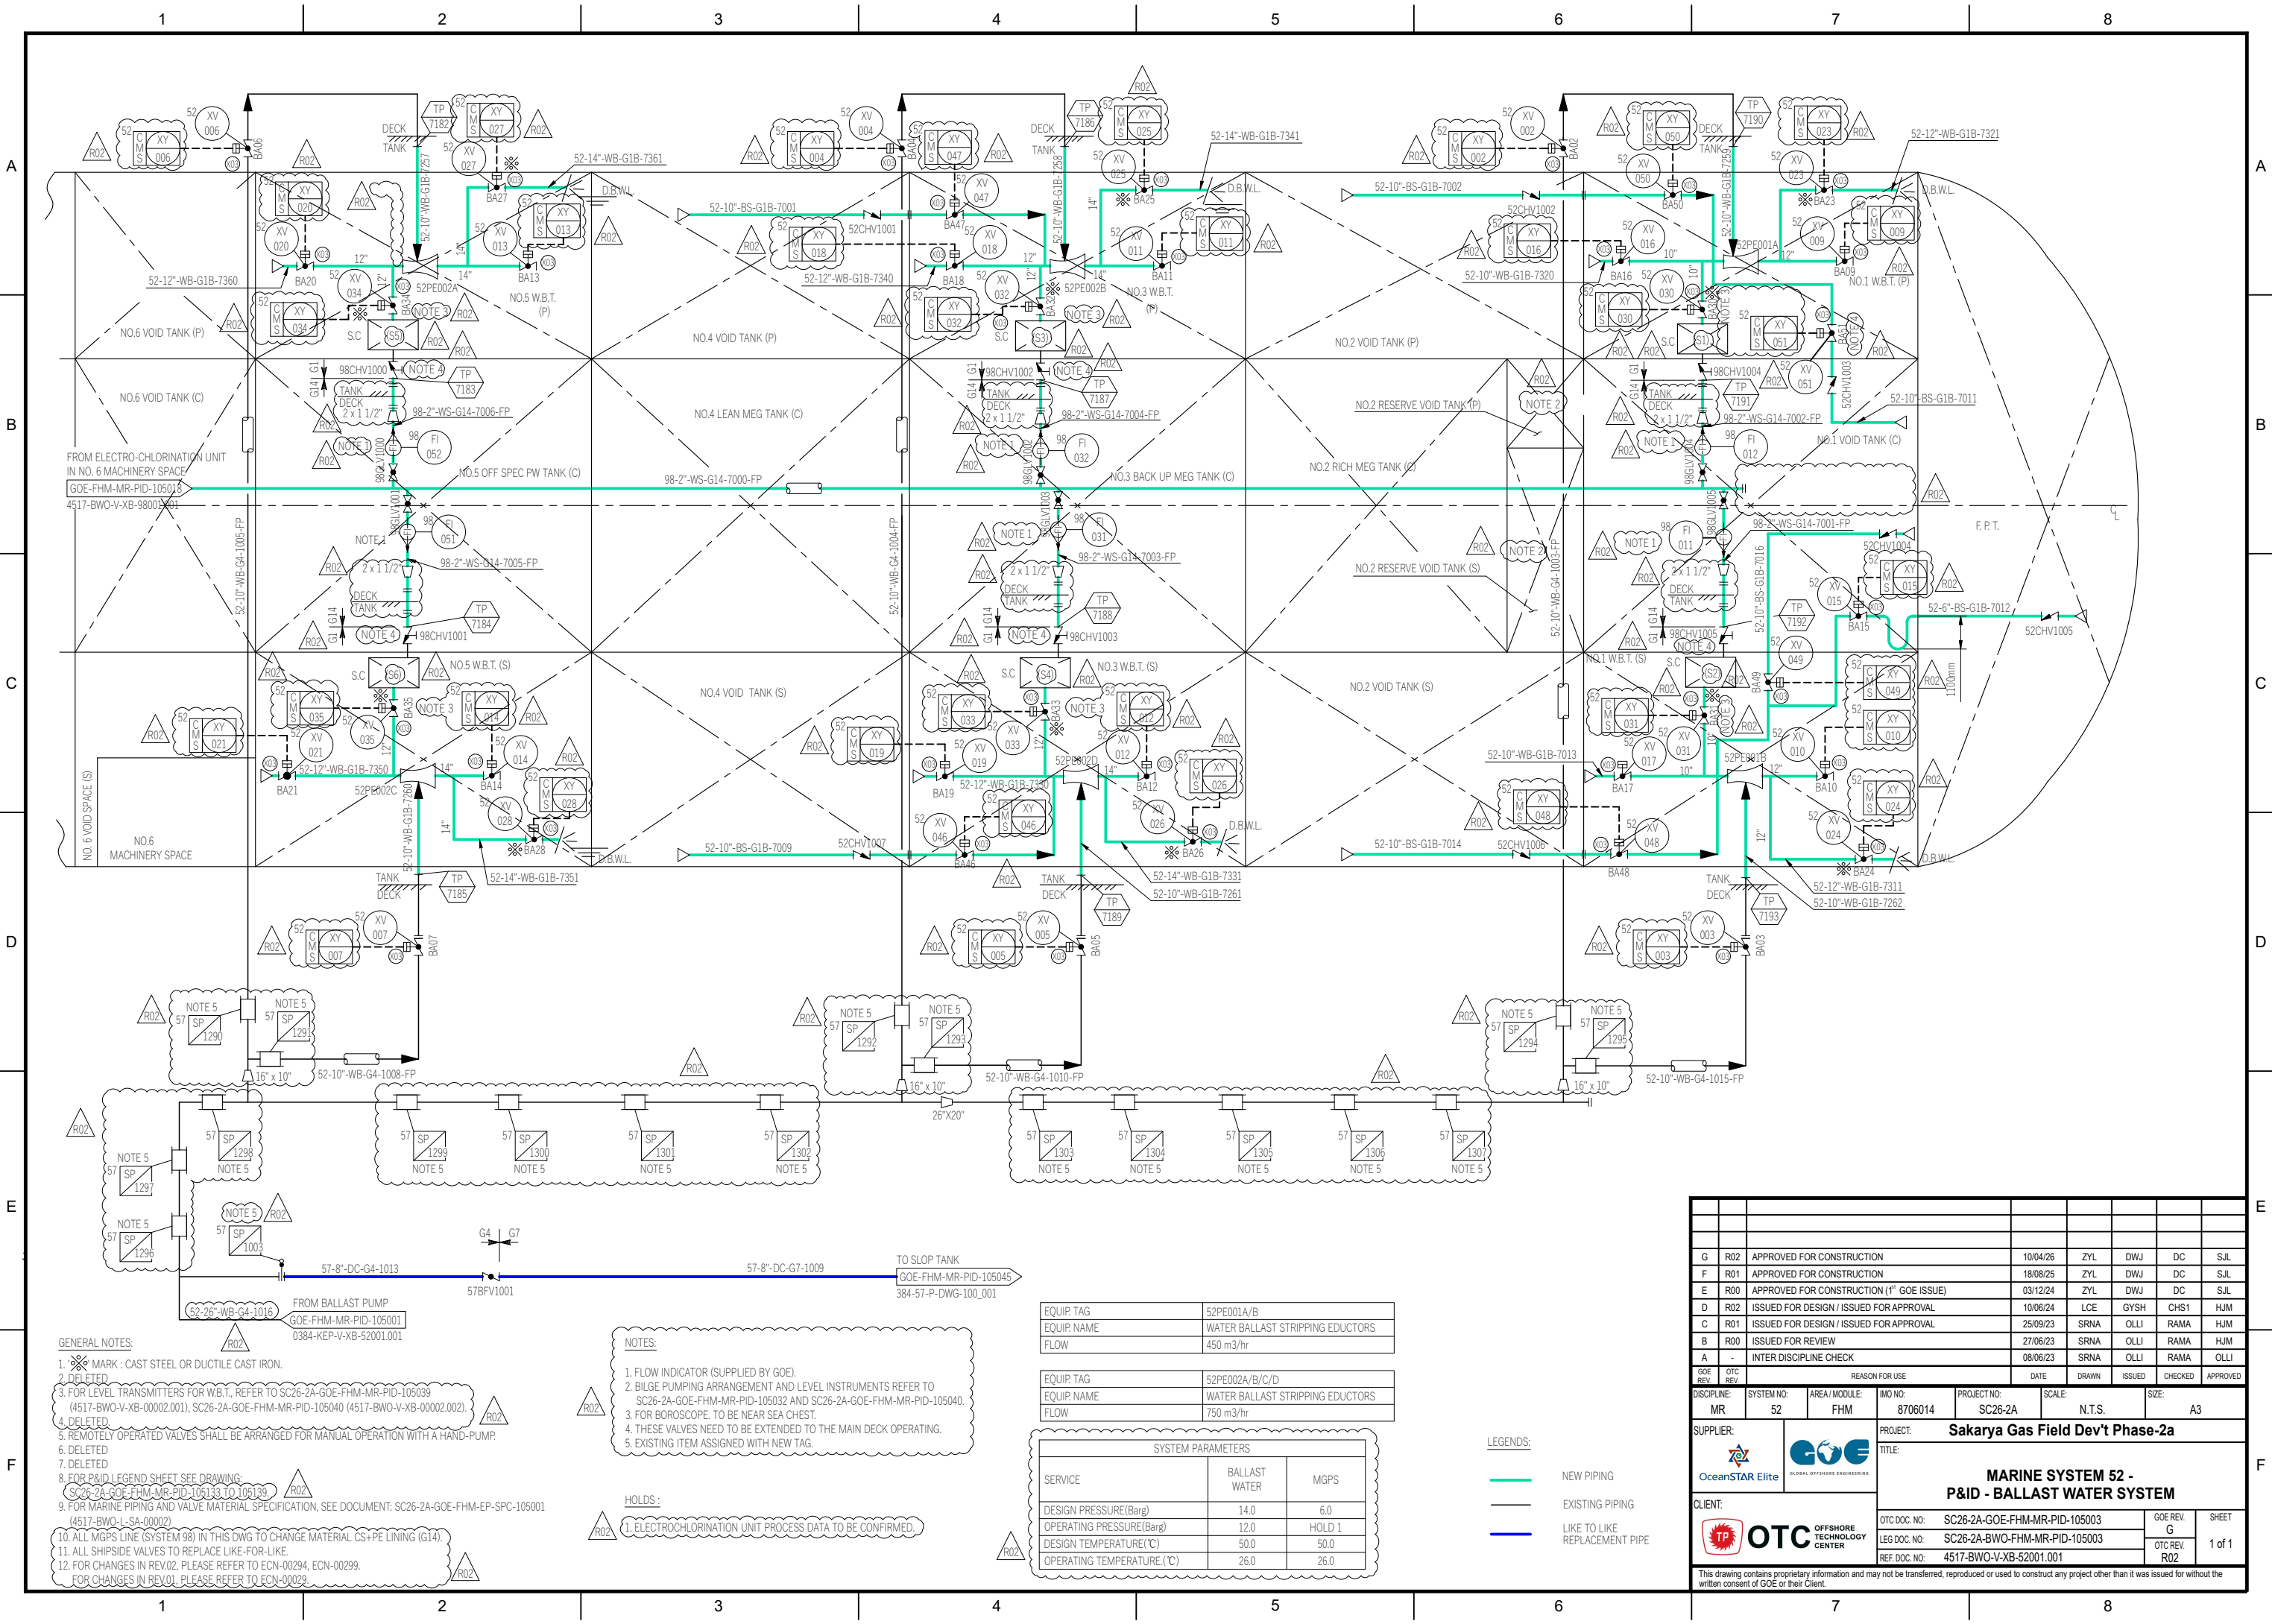

GENERAL NOTES:

- ✕ MARK : CAST STEEL OR DUCTILE CAST IRON.
- DELETED
- FOR LEVEL TRANSMITTERS FOR W.B.T., REFER TO SC26-2A-GOE-FHM-MR-PID-105039 (4517-BWO-V-XB-00002.001), SC26-2A-GOE-FHM-MR-PID-105040 (4517-BWO-V-XB-00002.002).
- DELETED
- REMOTELY OPERATED VALVES SHALL BE ARRANGED FOR MANUAL OPERATION WITH A HAND-PUMP.
- DELETED
- DELETED
- FOR P&ID LEGEND SHEET SEE DRAWING: SC26-2A-GOE-FHM-MR-PID-105133 TO 105139
- FOR MARINE PIPING AND VALVE MATERIAL SPECIFICATION, SEE DOCUMENT: SC26-2A-GOE-FHM-EP-SPC-105001 (4517-BWO-L-SA-00002)
- ALL MGPS LINE (SYSTEM 98) IN THIS DWG TO CHANGE MATERIAL CS+PE LINING (G14).
- ALL SHIPSIDE VALVES TO REPLACE LIKE-FOR-LIKE.
- FOR CHANGES IN REV02, PLEASE REFER TO ECN-00294, ECN-00299.
- FOR CHANGES IN REV01, PLEASE REFER TO ECN-00029.

NOTES:

- FLOW INDICATOR (SUPPLIED BY GOE).
- BILGE PUMPING ARRANGEMENT AND LEVEL INSTRUMENTS REFER TO SC26-2A-GOE-FHM-MR-PID-105032 AND SC26-2A-GOE-FHM-MR-PID-105040.
- FOR BOROSCOPE, TO BE NEAR SEA CHEST.
- THESE VALVES NEED TO BE EXTENDED TO THE MAIN DECK OPERATING.
- EXISTING ITEM ASSIGNED WITH NEW TAG.

HOLDS:

- ELECTROCHLORINATION UNIT PROCESS DATA TO BE CONFIRMED.

EQUIP. TAG	52PE001A/B	
EQUIP. NAME	WATER BALLAST STRIPPING EDUCTORS	
FLOW	450 m3/hr	

EQUIP. TAG	52PE002A/B/C/D	
EQUIP. NAME	WATER BALLAST STRIPPING EDUCTORS	
FLOW	750 m3/hr	

SYSTEM PARAMETERS		
SERVICE	BALLAST WATER	MGPS
DESIGN PRESSURE(Barg)	14.0	6.0
OPERATING PRESSURE(Barg)	12.0	HOLD 1
DESIGN TEMPERATURE(°C)	50.0	50.0
OPERATING TEMPERATURE(°C)	26.0	26.0

LEGENDS:

- NEW PIPING
- EXISTING PIPING
- LIKE TO LIKE REPLACEMENT PIPE

	</
--	--	----