
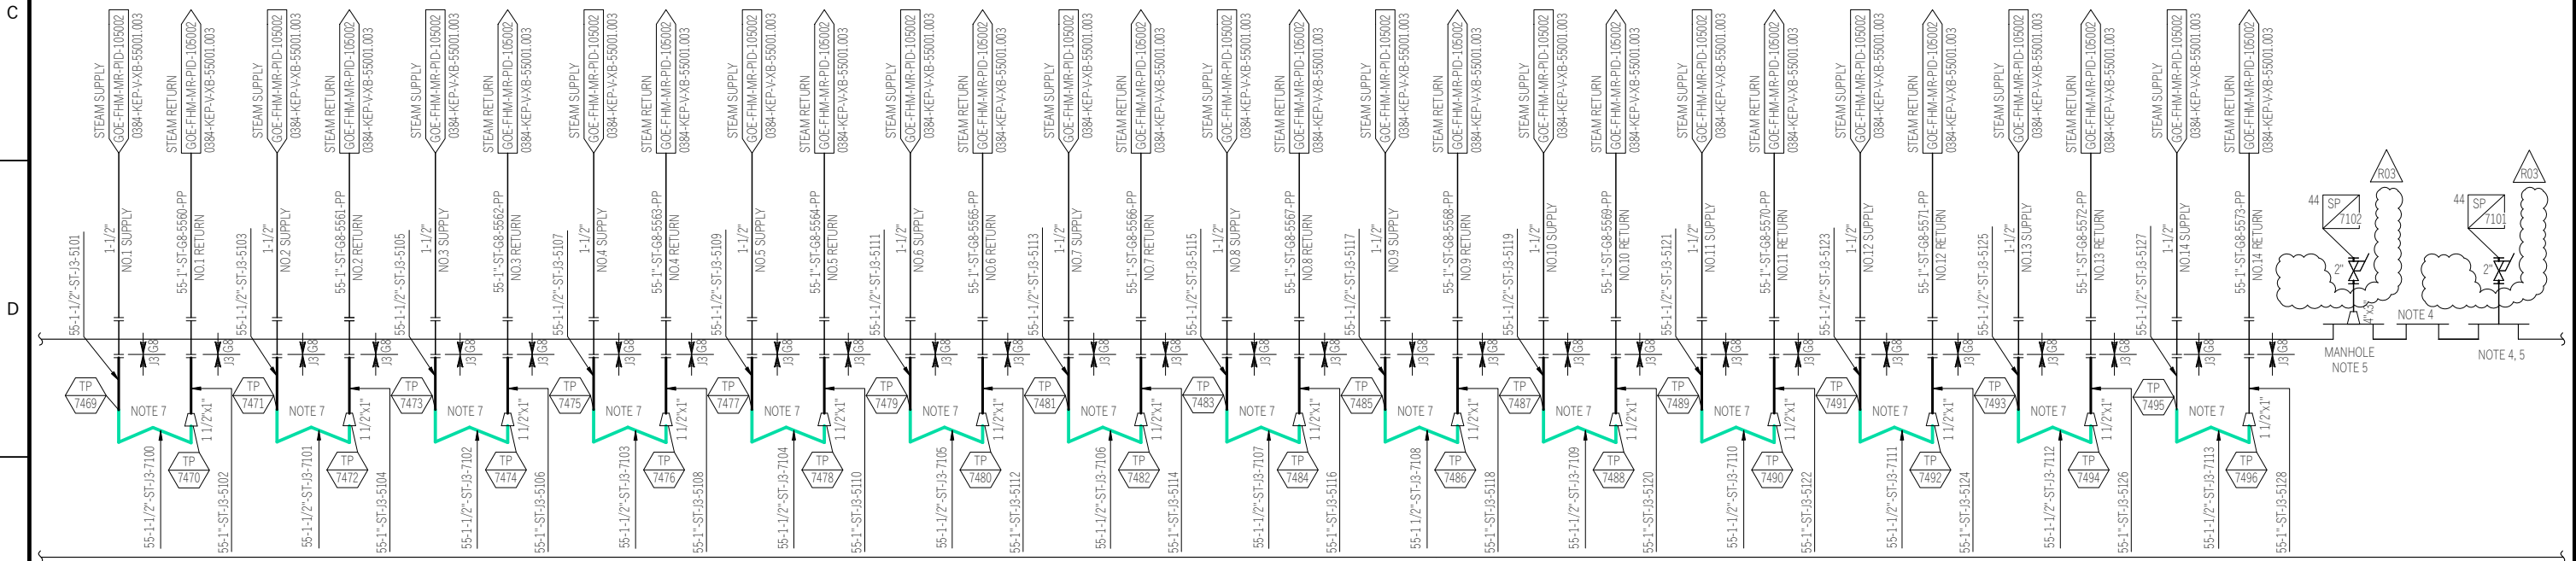


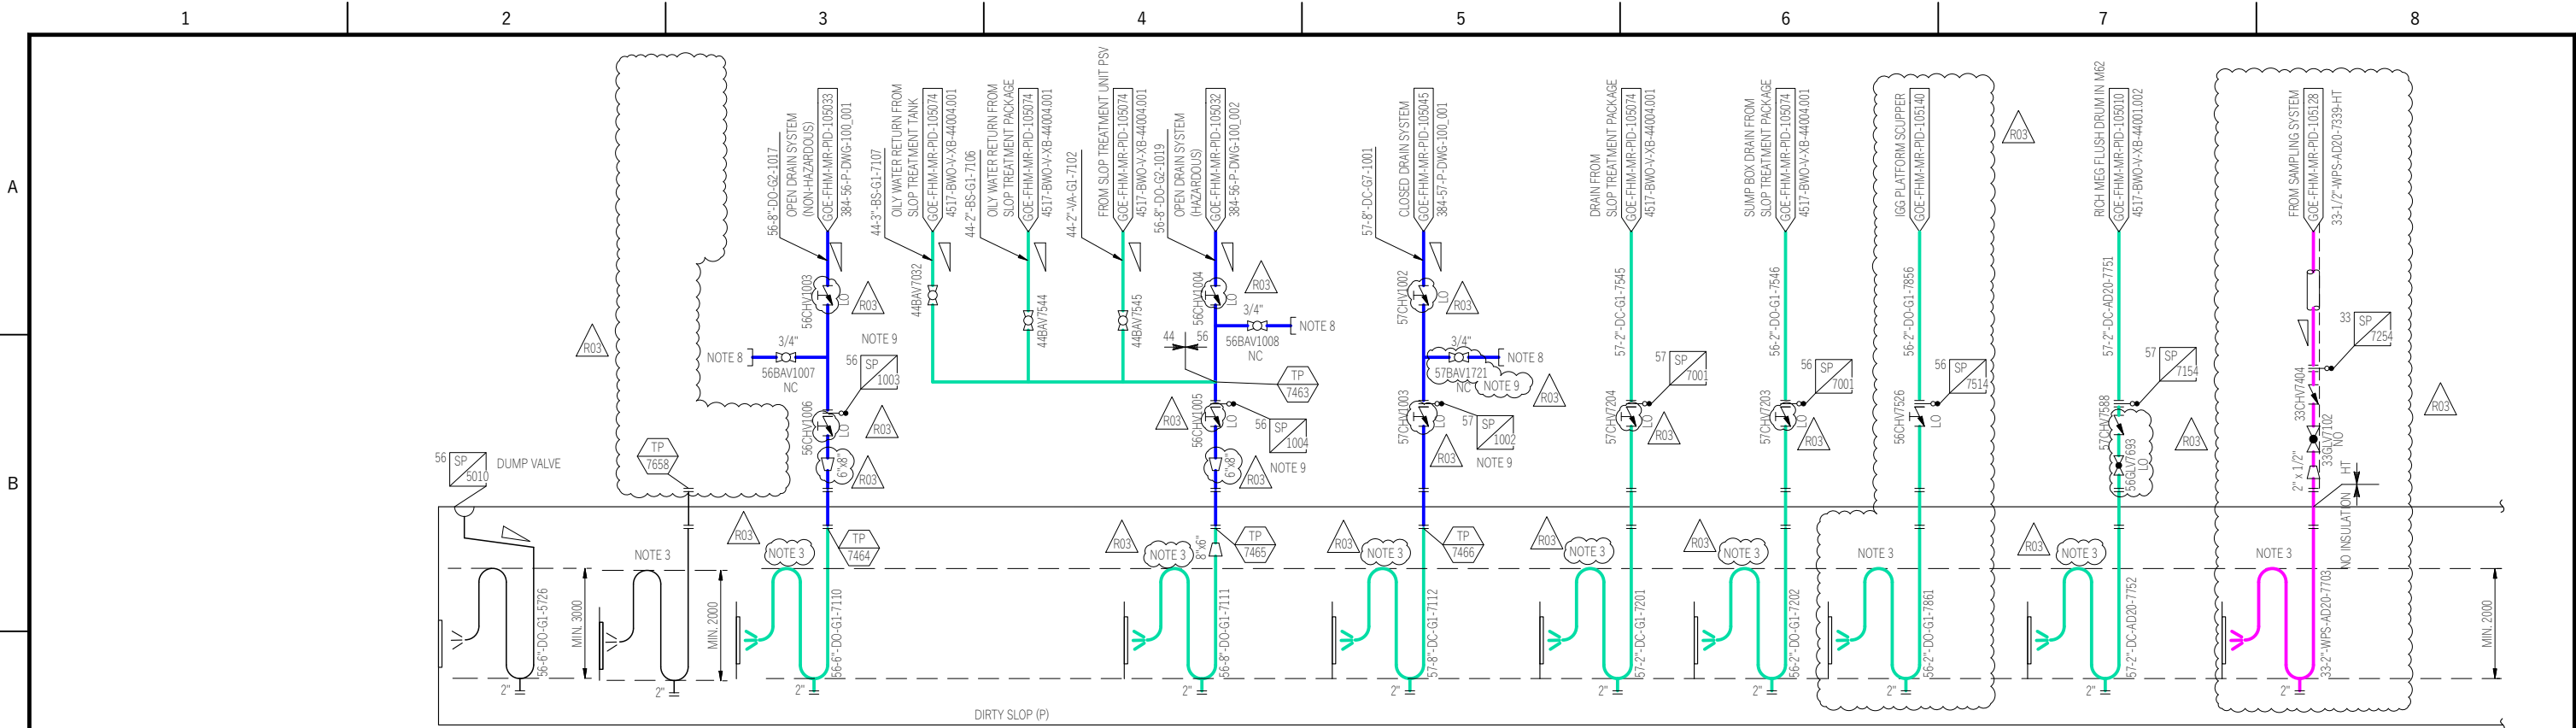

GENERAL NOTES:

- FOR P&ID LEGEND SHEET SEE DRAWING: SC26-2A-GOE-FHM-MR-PID-105002 TO 105139
- FOR MARINE PIPING AND VALVE MATERIAL SPECIFICATION, SEE DOCUMENT: SC26-2A-GOE-FHM-EP-SPC-105001 (4517-BWO-L-SA-00002)
- FOR CHANGES IN REV03, PLEASE REFER TO ECN-00296, ECN-00445. FOR CHANGES IN REV02, PLEASE REFER TO ECN-00268.

NOTES:

- DELETED.
- DELETED.
- TO HAVE A HOLE ON TOP OF U-SEAL IN SLOP TANK TO ACT AS SYPHON BREAKER (DIA. 15 MM FOR 2" PIPE AND DIA. 25 MM FOR ABOVE).
- HATCH FOR PORTABLE CLEANING MACHINE
- VAPOR LOCK VALVE (50A) FOR SOUNDING/SAMPLING. LOCATED ON THE EXISTING TANK NOZZLES. THE EXACT LOCATION TO BE DECIDED DURING DETAIL ENGINEERING.
- DELETED.
- HEATING COILS HAVE BEEN PARTIALLY INSTALLED DURING NEW AFT HULL PROJECT. REFER TO EXISTING ISOMETRIC DRAWING (0384-KEP-L-XN-00004.001) FOR HEATING COIL IN SLOP TANK (P). TO CONNECT THE DIS-JOINTED COILS AS PER SAKARYA HEATING COIL ISOMETRIC DRAWING (4517-HOLD 1).
- DETAILS OF UTILITY CONNECTION FOR CLEANING SHOWN IN DETAIL A
- EXISTING ITEM ASSIGNED WITH NEW TAG.

DETAIL A

SYSTEM PARAMETERS

SERVICE	CLOSED DRAIN	HAZARDOUS OPEN DRAIN	NON HAZARDOUS OPEN DRAIN	STEAM	SLOP
DESIGN PRESSURE(Barg)	15	8.6	8.9	11	15.5
OPERATING PRESSURE(Barg)	11-12	5	4.1	10	11-14
DESIGN TEMPERATURE(°C)	80	50	50	187	60
OPERATING TEMPERATURE(°C)	40	AMB	AMB	183	35

LEGENDS:

- EXISTING PIPE
- NEW PIPE
- LIKE TO LIKE REPLACEMENT PIPE
- SAMPLING PIPE

HOLD:

- DELETED
- DELETED
- DELETED
- DELETED
- DELETED

DISCIPLINE	MR	SYSTEM NO.	44	AREA / MODULE	FHM	IMO NO.	8706014	PROJECT NO.	SC26-2A	SCALE	N.T.S.	SIZE	A3
SUPPLIER:						PROJECT: Sakarya Gas Field Dev't Phase-2a							
CLIENT:						TITLE: MARINE SYSTEM 44 - P&ID SLOP TANK (P) (SHEET 2)							
OTC OFFSHORE TECHNOLOGY CENTER					OTC DOC. NO. SC26-2A-GOE-FHM-MR-PID-105011					GOE REV. H		SHEET 2 of 2	
					LEG DOC. NO. SC26-2A-BWO-FHM-MR-PID-105011					OTC REV. R03			
					REF DOC. NO. 4517-BWO-V-XB-44002.002								

This drawing contains proprietary information and may not be transferred, reproduced or used to construct any project other than it was issued for without the written consent of GOE or their Client.