


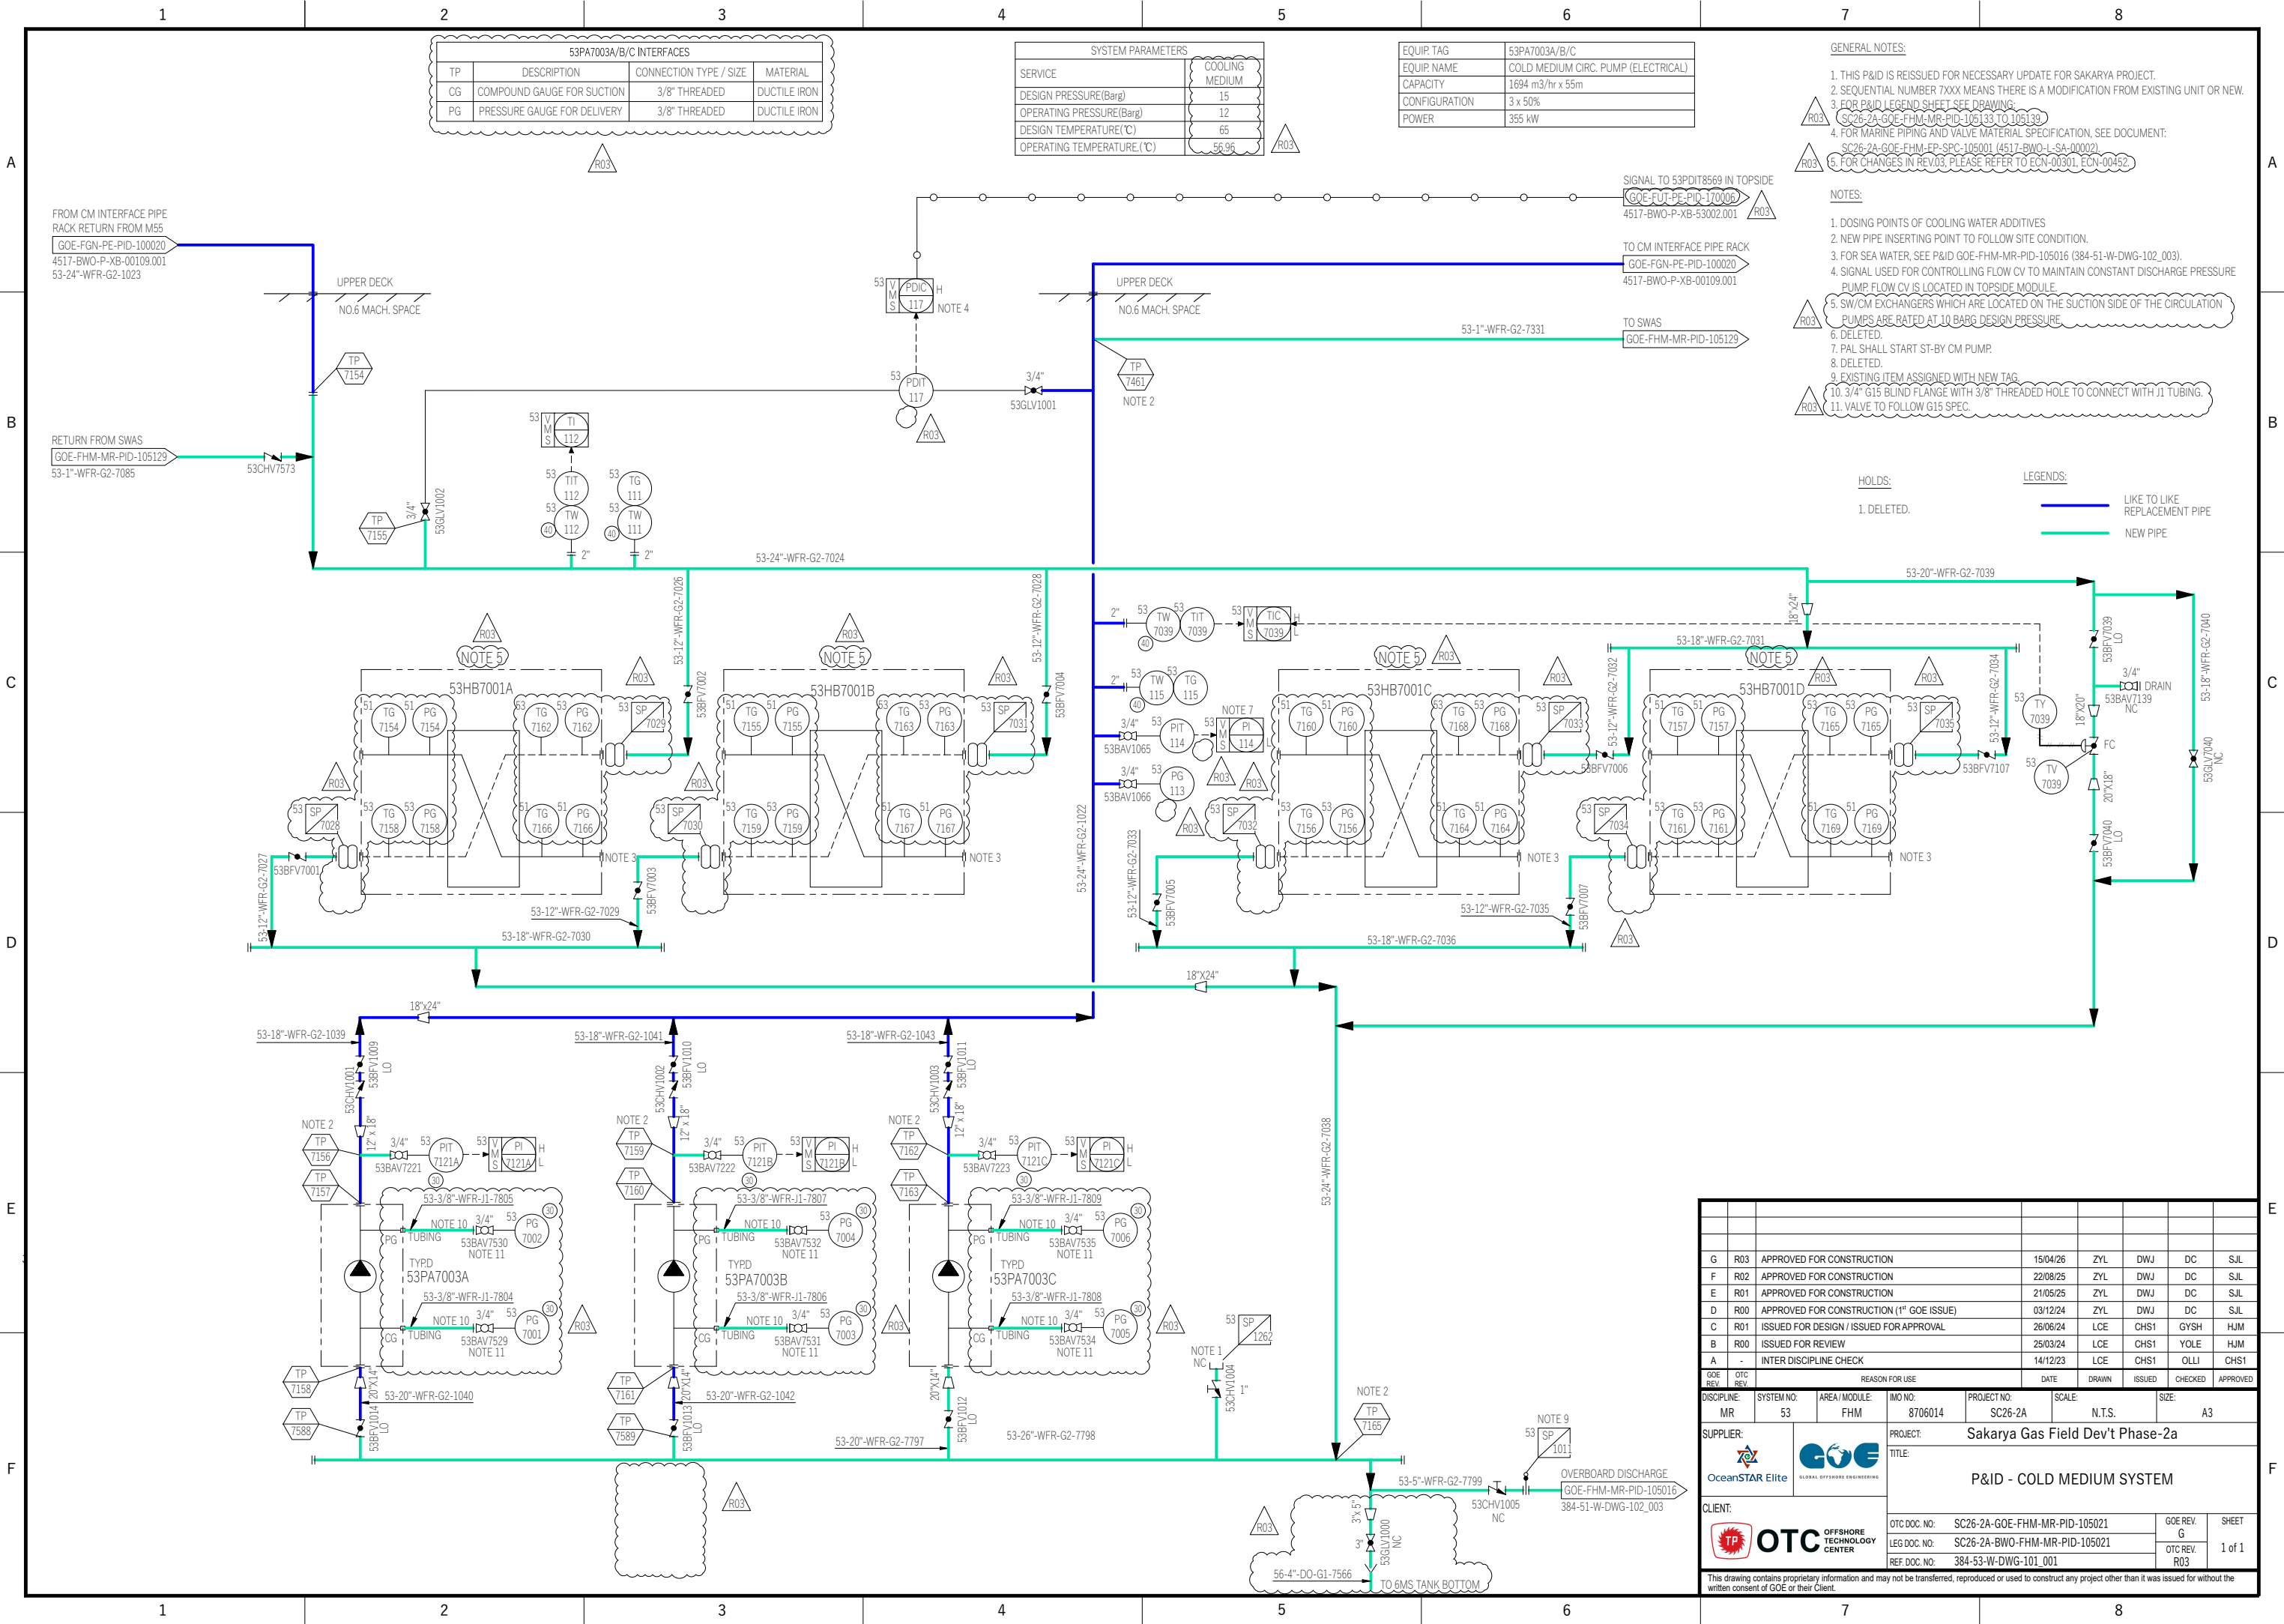

GENERAL NOTES:

- THIS P&ID IS REISSUED FOR NECESSARY UPDATE FOR SAKARYA PROJECT.
- SEQUENTIAL NUMBER 7XXX MEANS THERE IS A MODIFICATION FROM EXISTING UNIT OR NEW.
- FOR P&ID LEGEND SHEET SEE DRAWING.
- FOR MARINE PIPING AND VALVE MATERIAL SPECIFICATION, SEE DOCUMENT: SC26-2A-GOE-FHM-MR-PID-105133 TO 105138.
- FOR CHANGES IN REV03, PLEASE REFER TO ECN-00301, ECN-00452.

NOTES:

- DOSING POINTS OF COOLING WATER ADDITIVES
- NEW PIPE INSERTING POINT TO FOLLOW SITE CONDITION.
- FOR SEA WATER, SEE P&ID GOE-FHM-MR-PID-105016 (384-51-W-DWG-102_003).
- SIGNAL USED FOR CONTROLLING FLOW CV TO MAINTAIN CONSTANT DISCHARGE PRESSURE PUMP FLOW CV IS LOCATED IN TOPSIDE MODULE.
- SW/CM EXCHANGERS WHICH ARE RATED AT 10 BAR DESIGN PRESSURE.
- DELETED.
- PAL SHALL START ST-BY CM PUMP.
- DELETED.
- EXISTING ITEM ASSIGNED WITH NEW TAG.
10. 3/4" G15 BLIND FLANGE WITH 3/8" THREADED HOLE TO CONNECT WITH J1 TUBING.
- VALVE TO FOLLOW G15 SPEC.

HOLDS:

- DELETED.

LEGENDS:

- LIKE TO LIKE REPLACEMENT PIPE
- NEW PIPE

G	R03	APPROVED FOR CONSTRUCTION			15/04/26	ZYL	DWJ	DC	SJL	
F	R02	APPROVED FOR CONSTRUCTION			22/08/25	ZYL	DWJ	DC	SJL	
E	R01	APPROVED FOR CONSTRUCTION			21/05/25	ZYL	DWJ	DC	SJL	
D	R00	APPROVED FOR CONSTRUCTION (1 st GOE ISSUE)			03/12/24	ZYL	DWJ	DC	SJL	
C	R01	ISSUED FOR DESIGN / ISSUED FOR APPROVAL			26/06/24	LCE	CHS1	GYSH	HJM	
B	R00	ISSUED FOR REVIEW			25/03/24	LCE	CHS1	YOLE	HJM	
A	-	INTER DISCIPLINE CHECK			14/12/23	LCE	CHS1	OLLI	CHS1	
GOE REV	OTC REV	REASON FOR USE				DATE	DRAWN	ISSUED	CHECKED	APPROVED
DISCIPLINE:		SYSTEM NO.:	AREA / MODULE:	IMO NO.:	PROJECT NO.:	SCALE:	SIZE:			
MR		53	FHM	8706014	SC26-2A	N.T.S.	A3			
SUPPLIER:			PROJECT: Sakarya Gas Field Dev't Phase-2a							
 OceanSTAR Elite			 GLOBAL OFFSHORE ENGINEERING							
			TITLE: P&ID - COLD MEDIUM SYSTEM							
CLIENT:			OTC DOC. NO. SC26-2A-GOE-FHM-MR-PID-105021							
			OTC OFFSHORE TECHNOLOGY CENTER				GOE REV. G		SHEET	
			LEG DOC. NO. SC26-2A-BWO-FHM-MR-PID-105021				OTC REV. R03		1 of 1	
			REF DOC. NO. 384-53-W-DWG-101_001							
This drawing contains proprietary information and may not be transferred, reproduced or used to construct any project other than it was issued for without the written consent of GOE or their Client.										