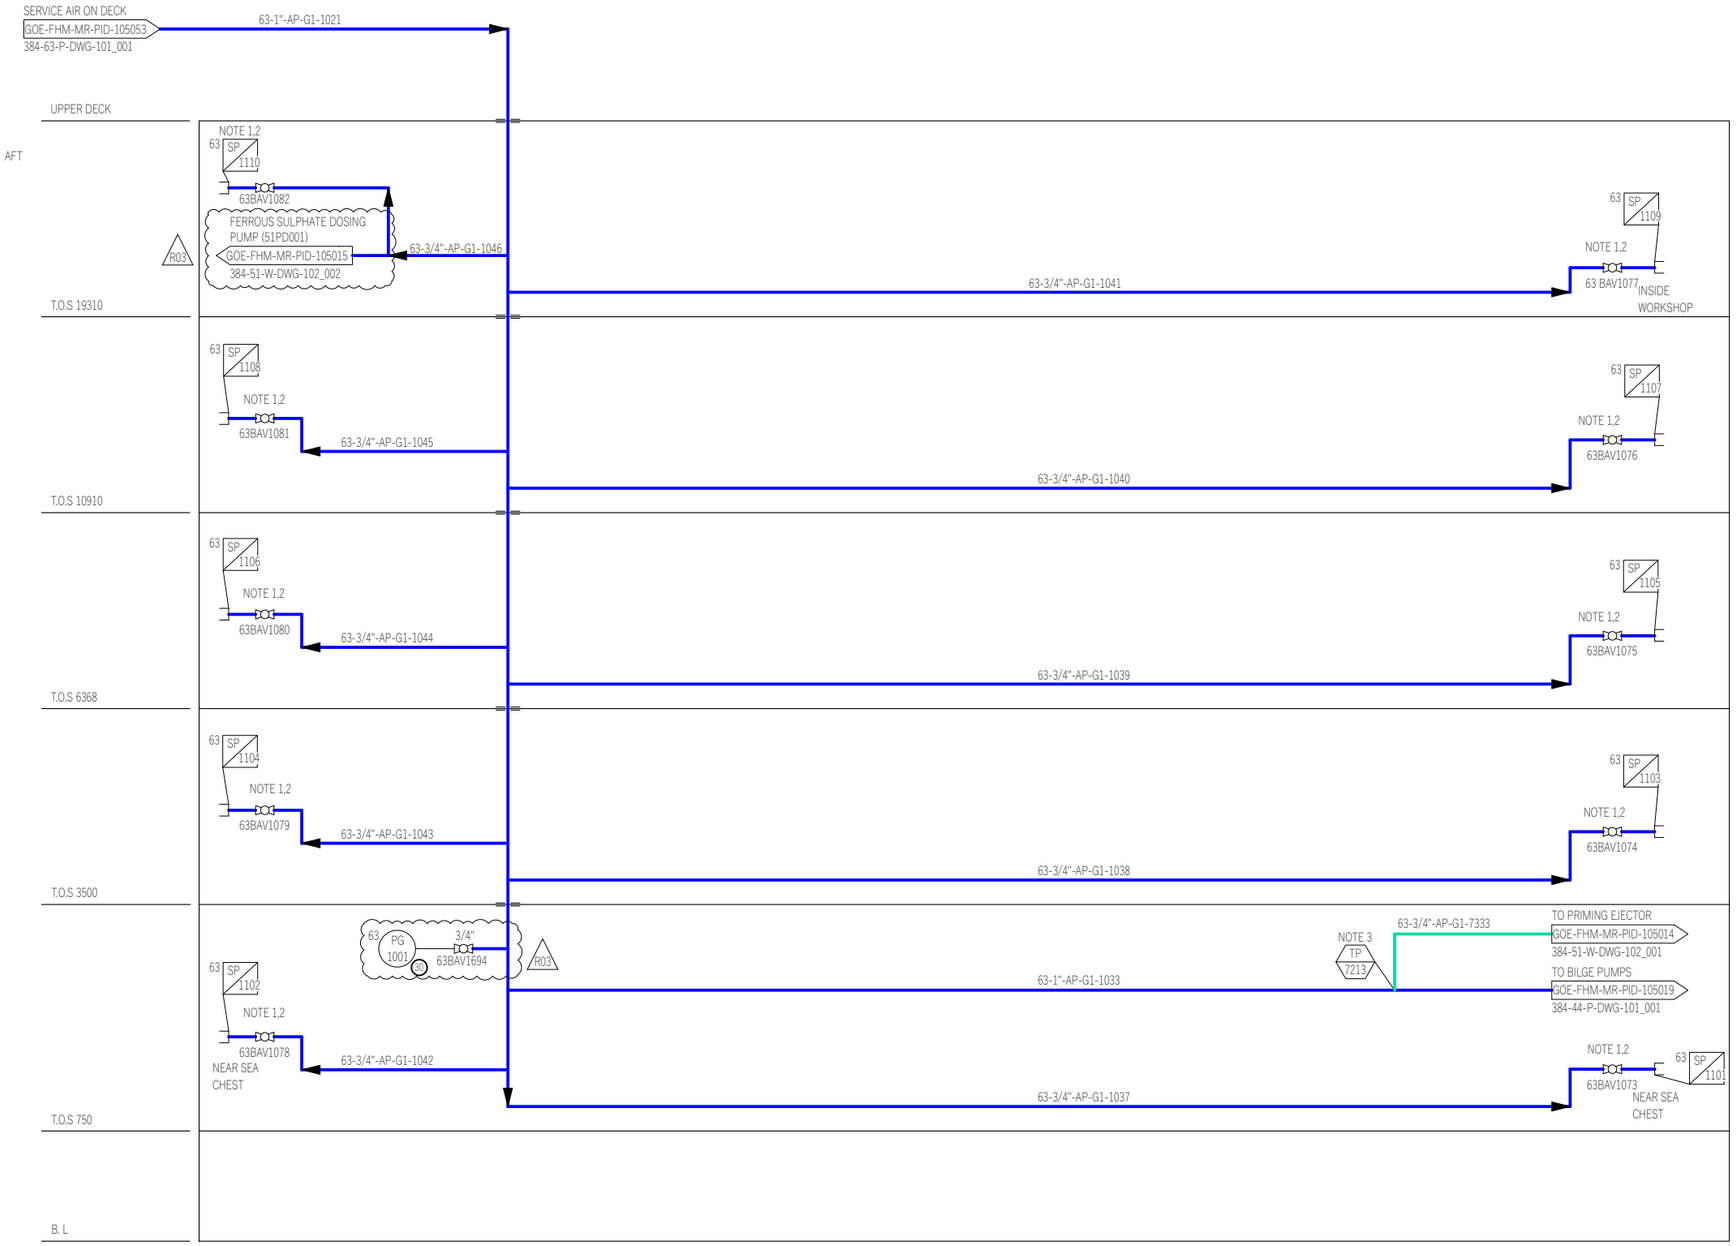



GENERAL NOTES:

1. THIS P&ID IS REISSUED FOR NECESSARY UPDATE FOR SAKARYA PROJECT.
2. SEQUENTIAL NUMBER 7XXX MEANS THERE IS A MODIFICATION FROM EXISTING UNIT OR NEW.
3. FOR P&ID LEGEND SHEET SEE DRAWING: SC26-2A-GOE-FGN-PE-PID-100018, SC26-2A-GOE-FGN-PE-PID-100021 TO 100031.
4. FOR MARINE PIPING AND VALVE MATERIAL SPECIFICATION, SEE DOCUMENT: SC26-2A-GOE-FHM-EP-SPC-105001 (4517-BWO-L-SA-00002).

R03 5. FOR CHANGES IN REV.03, PLEASE REFER TO ECN-00302. FOR CHANGES IN REV.01, PLEASE REFER TO ECN-00082.

NOTES:

1. TO PROVIDE TYPICAL UTILITY CONNECTION AS SHOWN BELOW. COMPLETE WITH 15 MTR LENGTH HOSE.

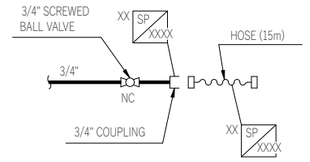

2. THERE WAS NO SI TAG NO. ON QUICK COUPLING FOR EXISTING UNIT. NEW TAG ASSIGNED WITH EXISTING TAG RANGE.
3. NEW PIPE INSERTING POINT TO FOLLOW SITE CONDITION.

LEGENDS:

- LIKE TO LIKE REPLACEMENT PIPE
- NEW PIPE

HOLDS:

1. DELETED.

SYSTEM PARAMETERS	
SERVICE	SERVICE AIR
DESIGN PRESSURE(Barg)	11.5
OPERATING PRESSURE(Barg)	10.0
DESIGN TEMPERATURE(°C)	50.0
OPERATING TEMPERATURE.(°C)	AMB

GOE REV.	OTC REV.	REASON FOR USE	DATE	DRAWN	ISSUED	CHECKED	APPROVED
G	R03	APPROVED FOR CONSTRUCTION	06/01/26	ZYL	DWJ	DC	SJL
F	R02	APPROVED FOR CONSTRUCTION	05/09/25	ZYL	DWJ	DC	SJL
E	R01	APPROVED FOR CONSTRUCTION	27/04/25	ZYL	DWJ	DC	SJL
D	R00	APPROVED FOR CONSTRUCTION (1st GOE ISSUE)	03/12/24	ZYL	DWJ	DC	SJL
C	R01	ISSUED FOR DESIGN / ISSUED FOR APPROVAL	04/06/24	LCE	GYSH	CHS1	HJM
B	R00	ISSUED FOR REVIEW	26/03/24	LCE	EIAN	CHS1	HJM
A	-	INTER DISCIPLINE CHECK	27/11/23	LCE	OLLI	CHS1	CHS1

DISCIPLINE:	SYSTEM NO:	AREA / MODULE:	IMO NO:	PROJECT NO:	SCALE:	SIZE:
MR	63	FHM	8706014	SC26-2A	N.T.S.	A3

SUPPLIER: OceanSTAR Elite / GOE GLOBAL OFFSHORE ENGINEERING

PROJECT: Sakarya Gas Field Dev't Phase-2a

TITLE: P&ID - SERVICE AIR IN NO.6 MACHINERY SPACE

CLIENT: TP OTC OFFSHORE TECHNOLOGY CENTER

OTC DOC. NO:	SC26-2A-GOE-FHM-MR-PID-105025	GOE REV.	SHEET
LEG DOC. NO:	SC26-2A-BWO-FHM-MR-PID-105025	G	1 of 1
REF. DOC. NO:	384-63-P-DWG-101_002	OTC REV. R03	

This drawing contains proprietary information and may not be transferred, reproduced or used to construct any project other than it was issued for without the written consent of GOE or their Client.