


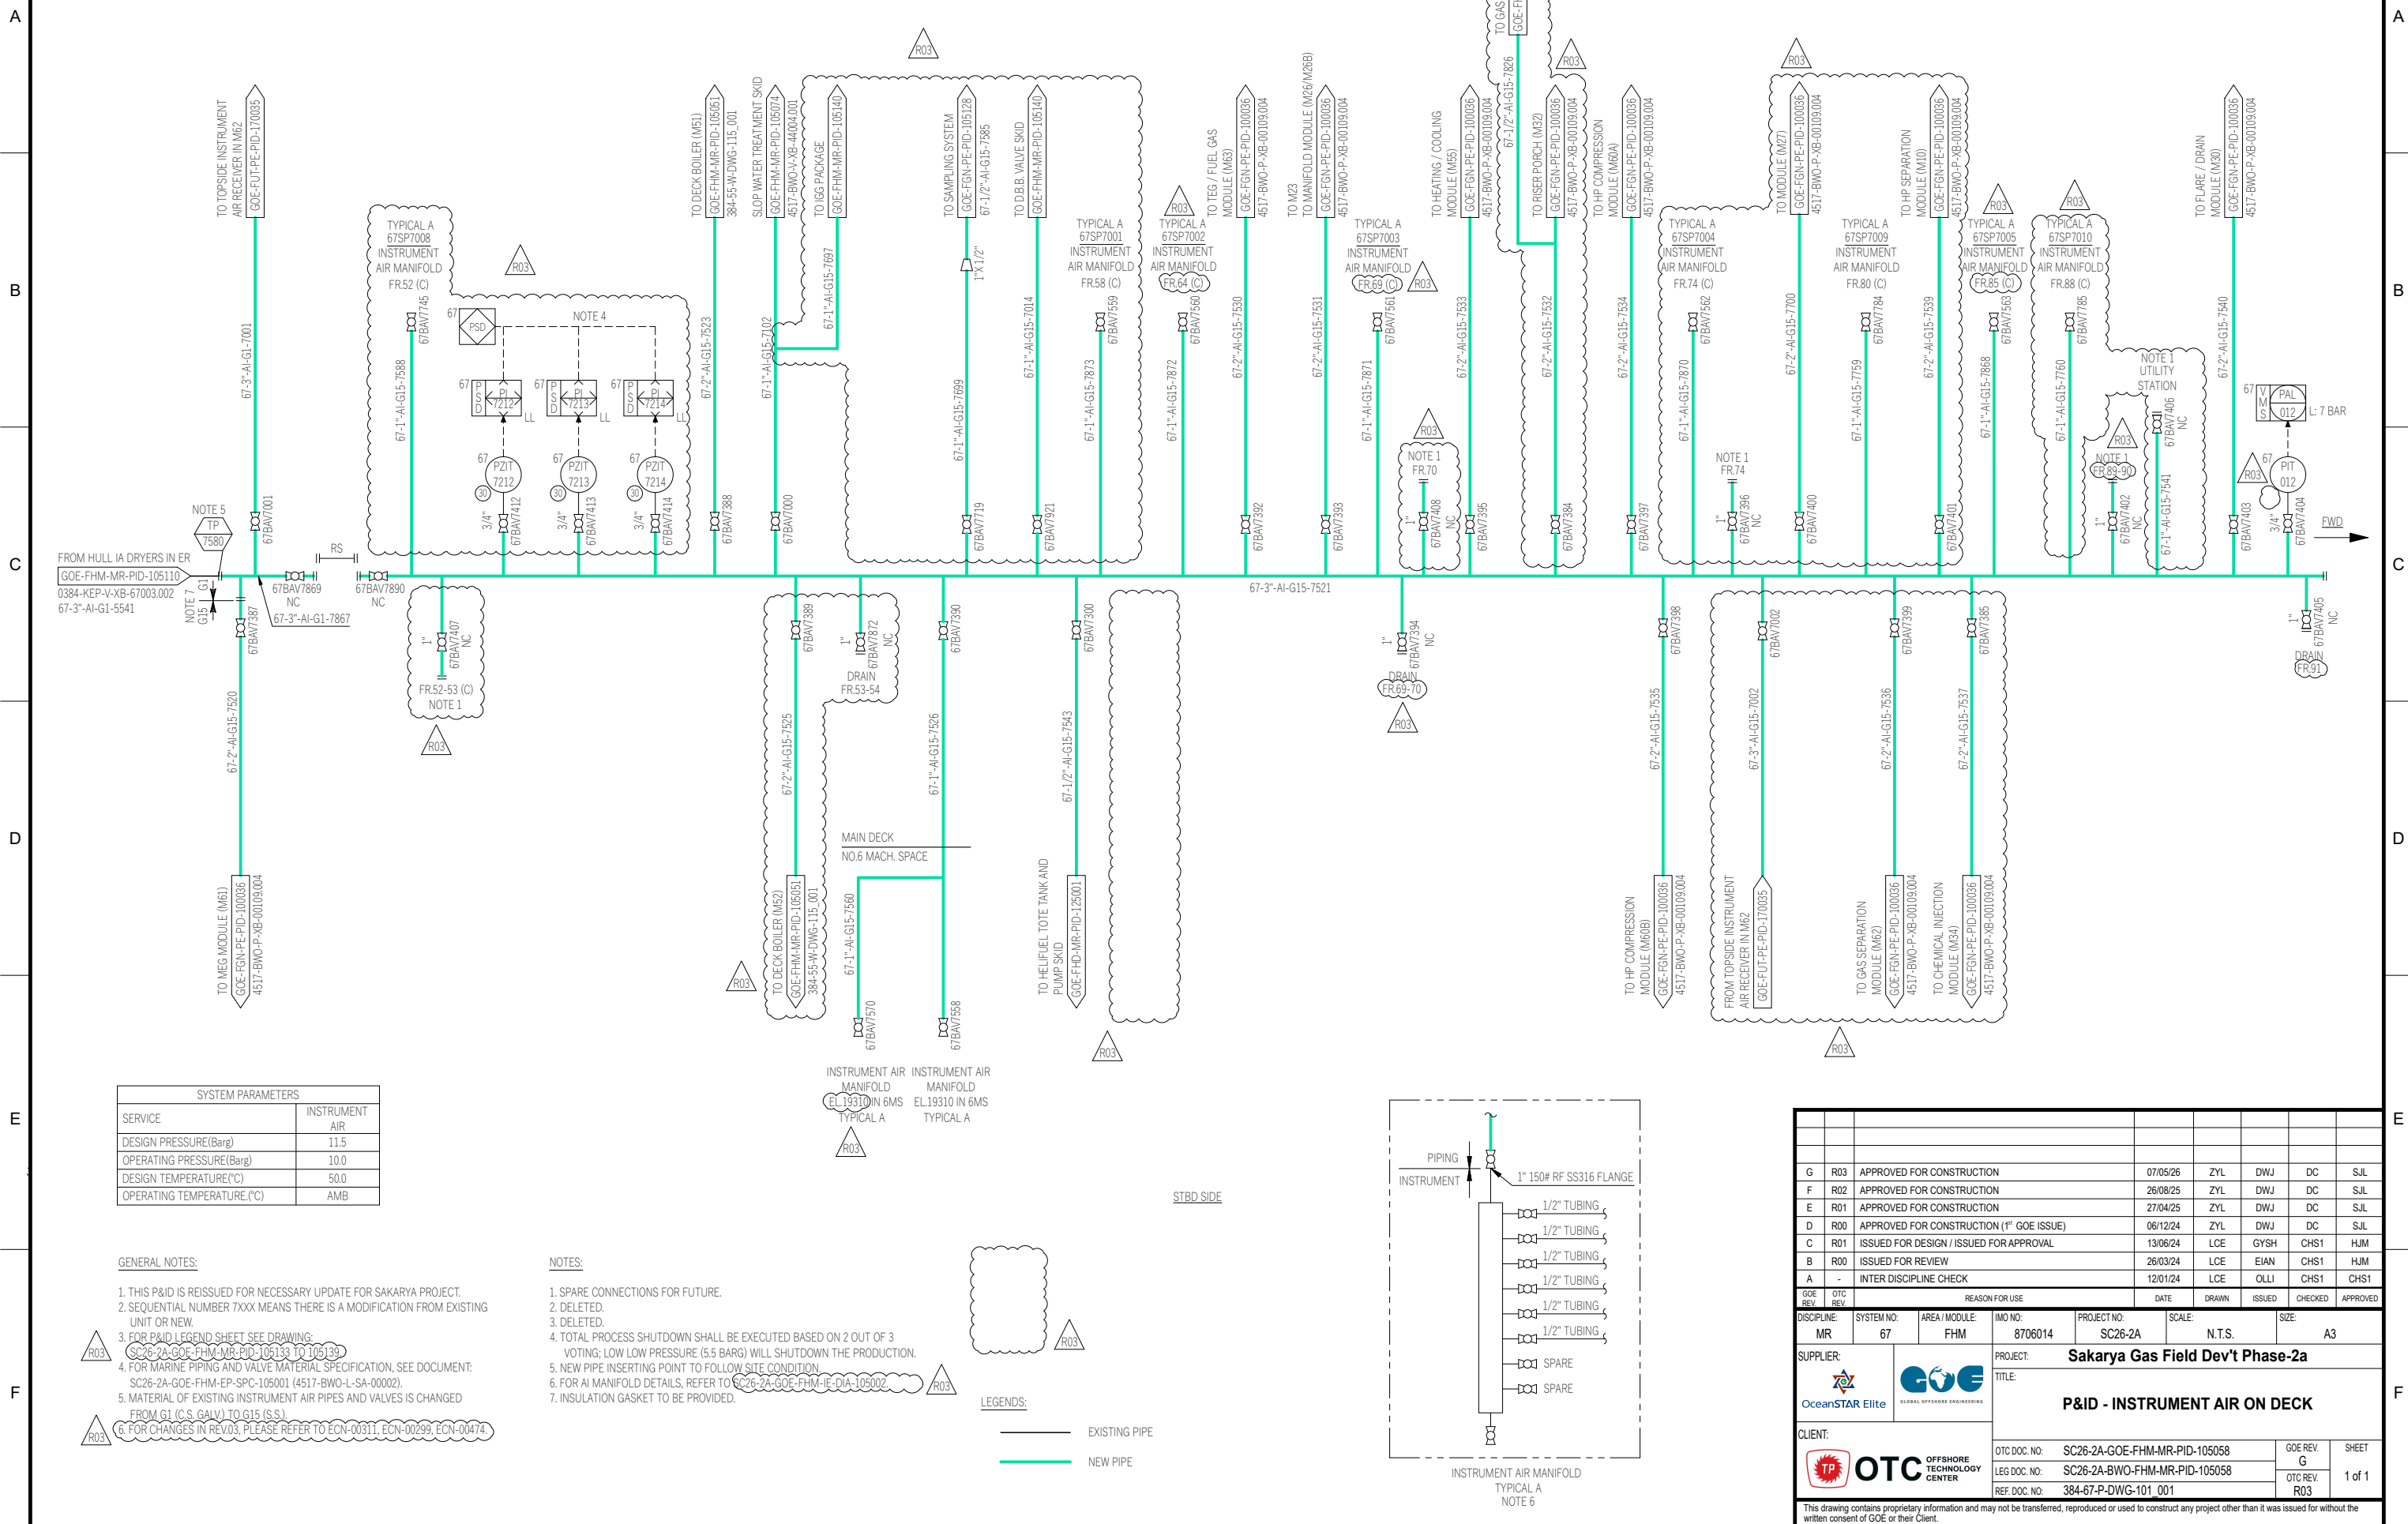

SYSTEM PARAMETERS	
SERVICE	INSTRUMENT AIR
DESIGN PRESSURE(Barg)	11.5
OPERATING PRESSURE(Barg)	10.0
DESIGN TEMPERATURE(°C)	50.0
OPERATING TEMPERATURE(°C)	AMB

GENERAL NOTES:


1. THIS P&ID IS REISED FOR NECESSARY UPDATE FOR SAKARYA PROJECT.
2. SEQUENTIAL NUMBER 7XXX MEANS THERE IS A MODIFICATION FROM EXISTING UNIT OR NEW.
3. FOR P&ID LEGEND SHEET SEE DRAWING:
SC26-2A-GOE-FHM-MK-PID-105133 TO 105139
4. FOR MARINE PIPING AND VALVE MATERIAL SPECIFICATION, SEE DOCUMENT:
SC26-2A-GOE-FHM-EP-SPC-105001 (4517-BWO-L-5A-00002).
5. MATERIAL OF EXISTING INSTRUMENT AIR PIPES AND VALVES IS CHANGED FROM G1 (C.S. GALV) TO G15 (S.S.).
6. FOR CHANGES IN REV03, PLEASE REFER TO ECN-00311, ECN-00299, ECN-00474.

NOTES:

1. SPARE CONNECTIONS FOR FUTURE.
2. DELETED.
3. DELETED.
4. TOTAL PROCESS SHUTDOWN SHALL BE EXECUTED BASED ON 2 OUT OF 3
VOTING: LOW LOW PRESSURE (5.5 BARG) WILL SHUTDOWN THE PRODUCTION.
5. NEW PIPE INSERTING POINT TO FOLLOW SITE CONDITION.
6. FOR AI MANIFOLD DETAILS, REFER TO SC26-2A-GOE-FHM-IF-DIA-105002.
7. INSULATION GASKET TO BE PROVIDED.

LEGENDS:

- EXISTING PIPE
— NEW PIPE

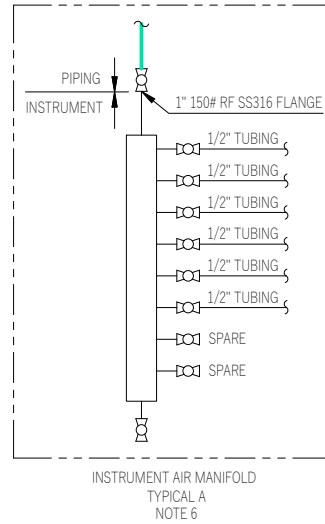

G	R03	APPROVED FOR CONSTRUCTION		07/05/26	ZYL	DWJ	DC	SJL	
F	R02	APPROVED FOR CONSTRUCTION		26/08/25	ZYL	DWJ	DC	SJL	
E	R01	APPROVED FOR CONSTRUCTION		27/04/25	ZYL	DWJ	DC	SJL	
D	R00	APPROVED FOR CONSTRUCTION (1 st GOE ISSUE)		06/12/24	ZYL	DWJ	DC	SJL	
C	R01	ISSUED FOR DESIGN / ISSUED FOR APPROVAL		13/06/24	LCE	GYSH	CHS1	HJM	
B	R00	ISSUED FOR REVIEW		26/03/24	LCE	EIAN	CHS1	HJM	
A	-	INTER DISCIPLINE CHECK		12/01/24	LCE	OLLI	CHS1	CHS1	
GOE REV	OTC REV	REASON FOR USE			DATE	DRAWN	ISSUED	CHECKED	APPROVED
DISCIPLINE:		SYSTEM NO:	AREA / MODULE:	IMO NO:	PROJECT NO:	SCALE:	SIZE:		
MR		67	FHM	8706014	SC26-2A	N.T.S.	A3		
SUPPLIER:				PROJECT: Sakarya Gas Field Dev't Phase-2a					
 OceanSTAR Elite				TITLE:					
 GLOBAL OFFSHORE ENGINEERING									
				P&ID - INSTRUMENT AIR ON DECK					
CLIENT:									
 OTC OFFSHORE TECHNOLOGY CENTER				OTC DOC. NO: SC26-2A-GOE-FHM-MR-PID-105058			GOE REV. G		SHEET 1 of 1
				LEG DOC. NO: SC26-2A-BWO-FHM-MR-PID-105058			OTC REV. R03		
				REF. DOC. NO: 384-67-P-DWG-101_001					
This drawing contains proprietary information and may not be transferred, reproduced or used to construct any project other than it was issued for without the written consent of GOE or their Client.									