


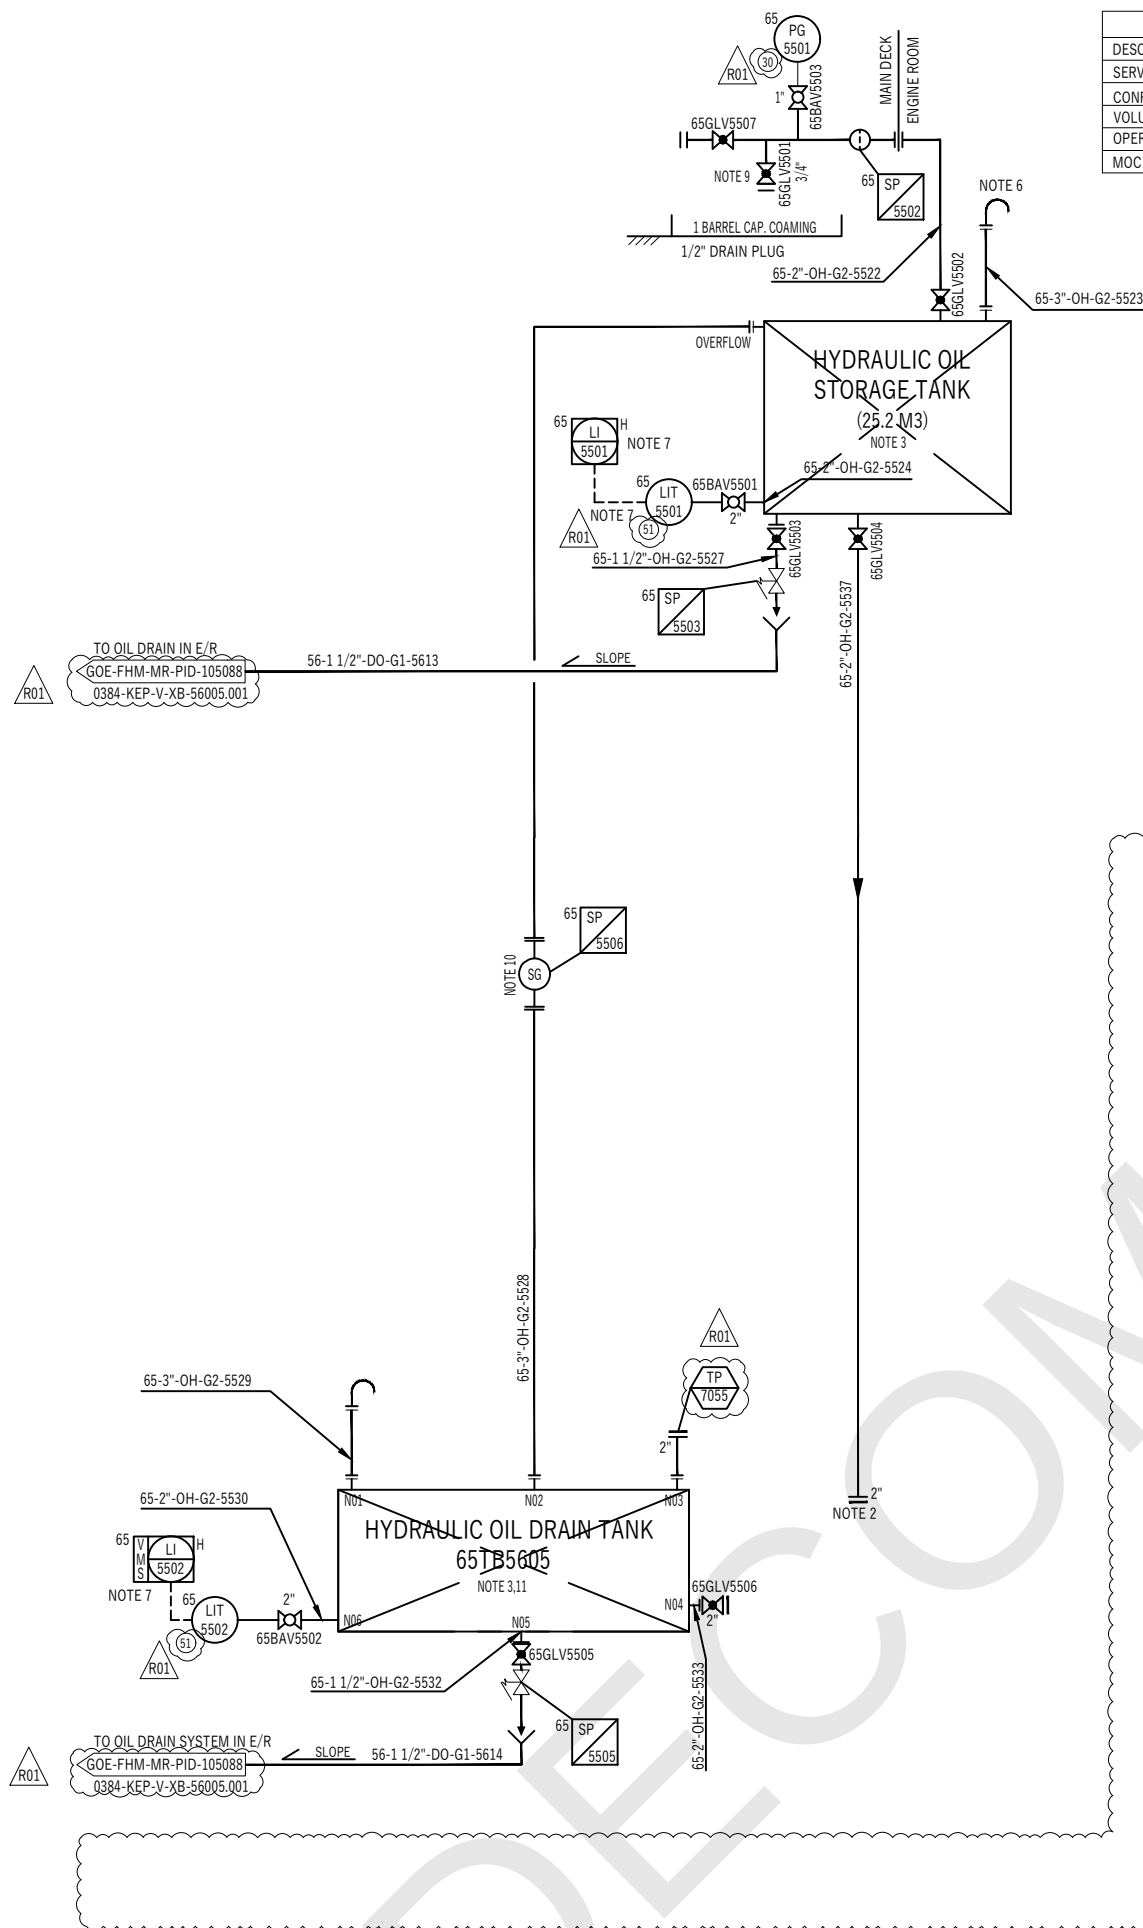

65TB5605	
DESCRIPTION	HYDRAULIC OIL DRAIN TANK
SERVICE	HYDRAULIC OIL
CONFIGURATION	1 x 100%
VOLUME	20 M3
OPERATING (DESIGN) PRESSURE	ATM (NOTE 3)
MOC	CARBON STEEL

GENERAL NOTES:

1. THIS P&ID UPDATED TO ALIGN SAKARYA DEEPWELL PUMP TYPE SELECTION (ELEC. DRIVEN). PREVIOUS P&ID WAS BASED ON HYD. OIL OPERATED TYPE.

NOTES

1. ~~DELETED.~~
2. FLANGES LOCATED AT HYD. OIL DRAIN TANK.
3. THE DESIGN PRESSURE SHALL BE HIGHER THAN STATIC PRESSURE.
4. ~~DELETED.~~
5. ~~DELETED.~~
6. LOCATION TO BE HIGHER THAN DAMAGE STABILITY LEVEL.
7. LEVEL TRANSMITTER TO BE DIFFERENTIAL PRESSURE TYPE.
8. ~~DELETED.~~
9. SAMPLING CONNECTION.
10. TO BE FITTED VERTICALLY AND EASILY ACCESSIBLE.
11. REFER TO 0384-KEP-N-XG-00115.001 FOR HPU DRAIN TANK DRAWING.

REFERENCES:

1. FOR P&ID LEGEND SHEET SEE DRAWING: SC26-2A-BWO-FGN-PE-PID-100018, SC26-2A-BWO-FGN-PE-PID-100021 TO 100031.
2. FOR MARINE PIPING AND VALVE MATERIAL SPECIFICATION, SEE DOCUMENT: SC26-2A-GOE-FHM-EP-SPC-105001 (4517-BWO-L-SA-00002).

HOLDS :

1. DELETED.

LEGENDS:

EXISTING PIPE

[illegible]