EQUIP. TAG	56PD5501
EQUIP. NAME	DECK DRAIN PUMP
CAPACITY	20 m3/h @ 2 barg
CONFIGURATION	1 x 100%
WORKING/DESIGN PRESSURE	2 / 8.9 BARG

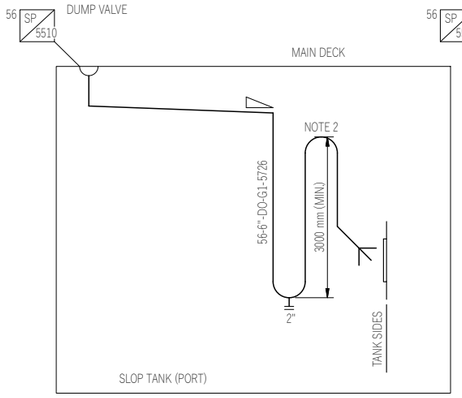

DETAIL 2

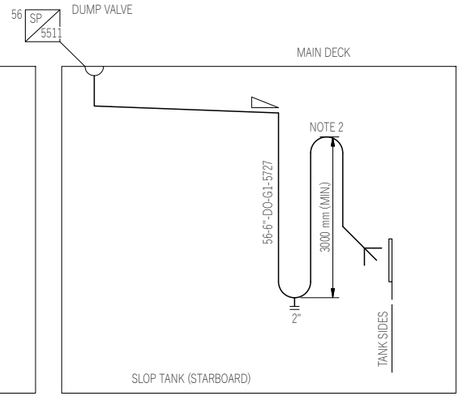

DETAIL 3

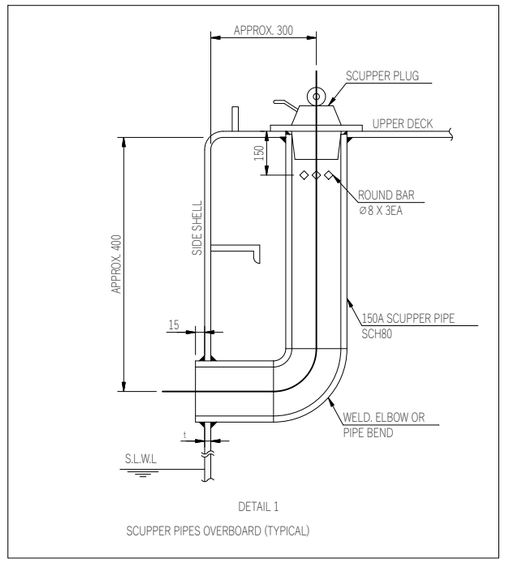

DETAIL 1

SCUPPER PIPES OVERBOARD (TYPICAL)

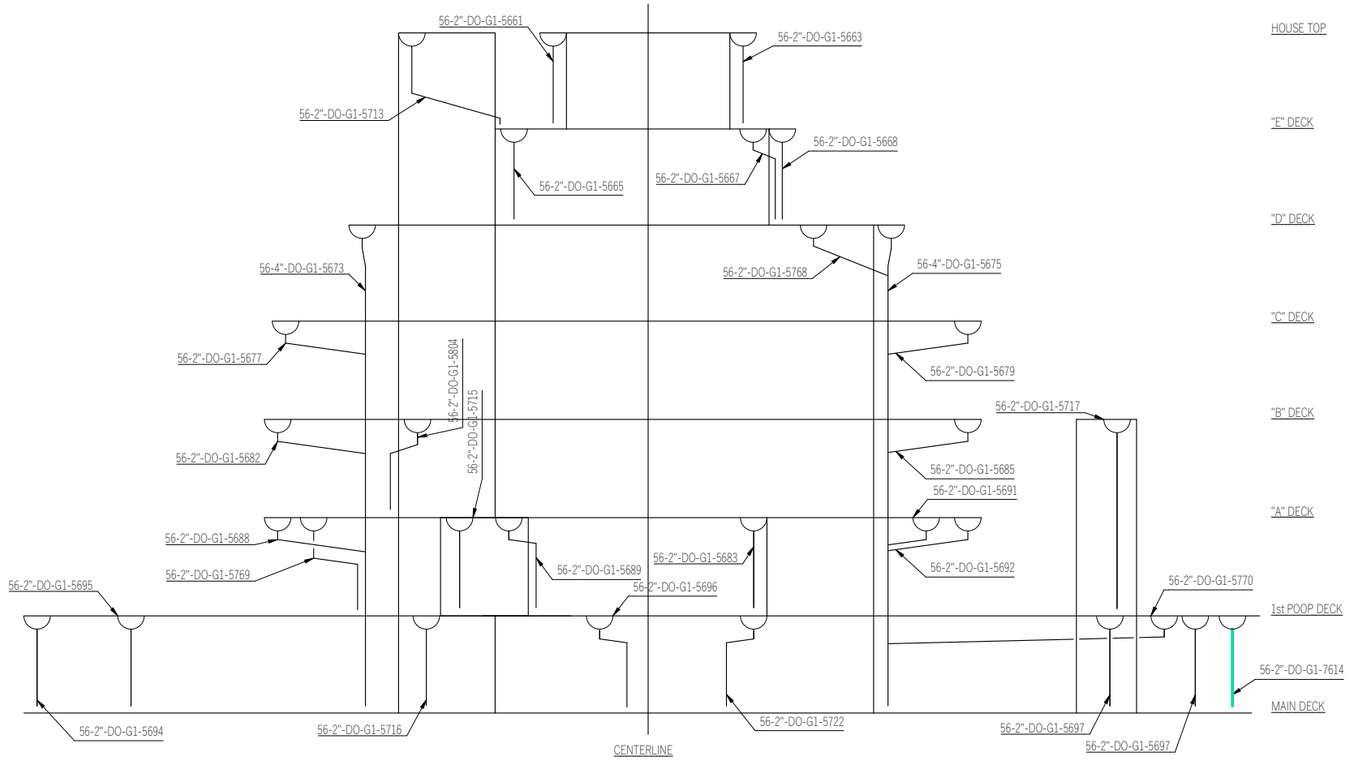

SECTION VIEW (LOOKING FWD)

SYSTEM PARAMETERS		
SERVICE	NON HAZARDOUS OPEN DRAIN	SERVICE AIR
DESIGN PRESSURE(Barg)	8.9	11.5
OPERATING PRESSURE(Barg)	4.1	10
DESIGN TEMPERATURE(℃)	50	50
OPERATING TEMPERATURE.(℃)	AMB	AMB

R03

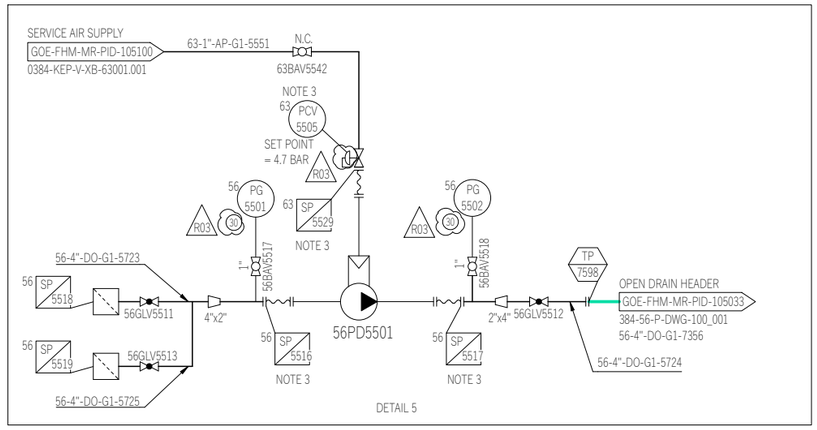

DETAIL 5

GENERAL NOTES:

1. THIS P&ID IS REISSUED FOR INFORMATION FOR SAKARYA PROJECT.
2. NO CHANGE IN SYSTEM.
3. FOR P&ID LEGEND SHEET SEE DRAWING:
   R03 SC26-2A-GOE-FHM-MR-PID-105133 TO 105139.
4. FOR MARINE PIPING AND VALVE MATERIAL SPECIFICATION, SEE DOCUMENT:
   SC26-2A-GOE-FHM-EP-SPC-105001 (4517-BWO-1-SA-00002).
5. FOR CHANGES IN REV.03, PLEASE REFER TO ECN-00319, ECN-00436.
   R03

NOTE:

1. REFER TO PIPING CONSTRUCTION STANDARD FOR SCUPPER DETAILS.
2. TO HAVE A HOLE OF 1" ON TOP OF THE U SEAL IN SLOP TANK TO ACT AS SIPHON BREAKER.
3. VENDOR SUPPLIED.

LEGENDS:

EXISTING PIPE

NEW PIPE

GOE REV.	OTC REV.	REASON FOR USE	DATE	DRAWN	ISSUED	CHECKED	APPROVED
-	R03	ISSUED FOR INFORMATION	20/04/26	ZYL	DWJ	DC	SJL
-	R02	ISSUED FOR INFORMATION	05/09/25	ZYL	DWJ	DC	SJL
-	R01	ISSUED FOR INFORMATION	14/05/25	ZYL	DWJ	DC	SJL
-	R00	ISSUED FOR INFORMATION (1ST GOE ISSUE)	26/12/24	ZYL	DWJ	DC	SJL
Z2	-	RE-ISSUED FOR AS-BUILT	31/01/23	EM	ADB	NO	PL
Z1	-	RE-ISSUED FOR AS-BUILT	18/01/23	EM	ADB	NO	PL
Z0	-	ISSUED FOR AS-BUILT	28/09/22	JT	JT	NO	PL
04	-	RE-ISSUED FOR CONSTRUCTION	27/05/22	JT	JT	NO	PL
03	-	RE-ISSUED FOR CONSTRUCTION	05/01/22	XH	JT	NO	PL
02	-	RE-ISSUED FOR CONSTRUCTION	06/08/20	XH	JT	NO	PL
01	-	RE-ISSUED FOR CONSTRUCTION	20/02/20	XH	JT	NO	PL
00	-	ISSUED FOR CONSTRUCTION	13/12/19	XH	JT	NO	PL
C	-	ISSUED FOR DESIGN	29/10/19	XH	JT	NO	PL
B	-	ISSUED FOR REVIEW	26/08/19	XH	JT	NO	PL
A	-	ISSUED FOR IDC	07/07/19	XH	JT	NO	PL

DISCIPLINE:	SYSTEM NO:	AREA / MODULE:	IMO NO:	PROJECT NO:	SCALE:	SIZE:
MR	56	FLQ	8706014	SC26-2A	N.T.S.	A3

SUPPLIER: OceanSTAR Elite / GOE GLOBAL OFFSHORE ENGINEERING

CLIENT: OTC OFFSHORE TECHNOLOGY CENTER

PROJECT: Sakarya Gas Field Dev't Phase-2a

TITLE: P&ID - ACCOMMODATION OUTDOOR SCUPPER SYSTEM (SHEET 4)

OTC DOC. NO:	SC26-2A-GOE-FLQ-MR-PID-120007	GOE REV.	SHEET
LEG DOC. NO:	-	-	4 of 4
REF. DOC. NO:	0384-KEP-V-XB-56003.004	OTC REV. R03	

This drawing contains proprietary information and may not be transferred, reproduced or used to construct any project other than it was issued for without the written consent of GOE or their Client.