91MZ7000 INTERFACE			
TP	DESCRIPTION	CONNECTION TYPE / SIZE	MATERIAL
TP-01	MGO R03	4" ANSI B16.5 RF 150# WELD NECK FLANGE	CARBON STEEL
TP-02	FRESH WATER	4" ANSI B16.5 RF 150# WELD NECK FLANGE	SS 316L
TP-03	LEAN MEG	6" ANSI B16.5 RF 150# WELD NECK FLANGE	SS 316L R03
TP-04	SODIUM HYDROXIDE	3" ANSI B16.5 RF 150# WELD NECK FLANGE	SS 316L
TP-05	SODIUM CARBONATE	4" ANSI B16.5 RF 150# WELD NECK FLANGE	SS 316L
TP-06	OFF-SPEC PW	4" ANSI B16.5 RF 150# WELD NECK FLANGE	SS 316L R03

R03

91MZ7000 (NEW)	
DESCRIPTION	MGO, POTABLE WATER, MEG, SODIUM HYDROXIDE, SODIUM CARBONATE, OFF-SPEC WATER
SERVICE	BUNKER HOSE REEL SKID
CAPACITY	MGO: 80 M3/H (HOLD 4) R03 FRESH WATER: 80 M3/H (HOLD 4) LEAN MEG: 180 M3/H (HOLD 4) SODIUM HYDROXIDE: (HOLD 4) R02 SODIUM CARBONATE: (HOLD 4) OFF-SPEC PW: 150 m3/h

GENERAL NOTES :

1. FOR P&ID LEGEND SHEET SEE DRAWING: R03 SC26-2A-GOE-FHM-MR-PID-105133 TO 105139.
2. FOR MARINE PIPING AND VALVE MATERIAL SPECIFICATION SEE DOCUMENT: SC26-2A-GOE-FHM-EP-SPC-105001 (4517-BWO-L-SA-00002)
3. R03 FOR CHANGES IN REV.03, PLEASE REFER TO ECN-00308, ECN-00467. FOR CHANGES IN REV.01, PLEASE REFER TO ECN-00093.

NOTES:

1. FLOWMETER TOTALIZER WITH RESET FACILITY LOCALLY.
2. R03 4" MARPOL DRIP SAMPLER.
3. STRAINER TO HAVE DRAIN AND VENT VALVE (STRAINER VENDOR SUPPLY)
4. R03 DELETED.
5. EACH FILLING PIPING HAS AN INDEPENDENT HOSE REEL AND DRIP TRAY.
6. INSULATION KIT TO BE PROVIDED.
7. VALVES TO BE USED FOR HOSE FLUSHING.
8. R03 DRAIN VALVE FOR DRIP TRAY TO BE BLANKED AND SPILLAGE TO BE COLLECTED MANUALLY USING POTABLE AIR PUMP IF REQUIRED.
9. R03 SERVICE AIR FOR BLOWING THROUGH AFTER BUNKERING/DE-BUNKERING.

HOLDS:

1. DELETED
2. DELETED.
3. DELETED.
4. NEW EQUIPMENT INFO. TBC
5. DELETED.
6. DELETED.
7. OPERATING PRESSURE TO BE CONFIRMED.

LEGENDS:

- LIKE TO LIKE REPLACEMENT PIPE
- NEW PIPE

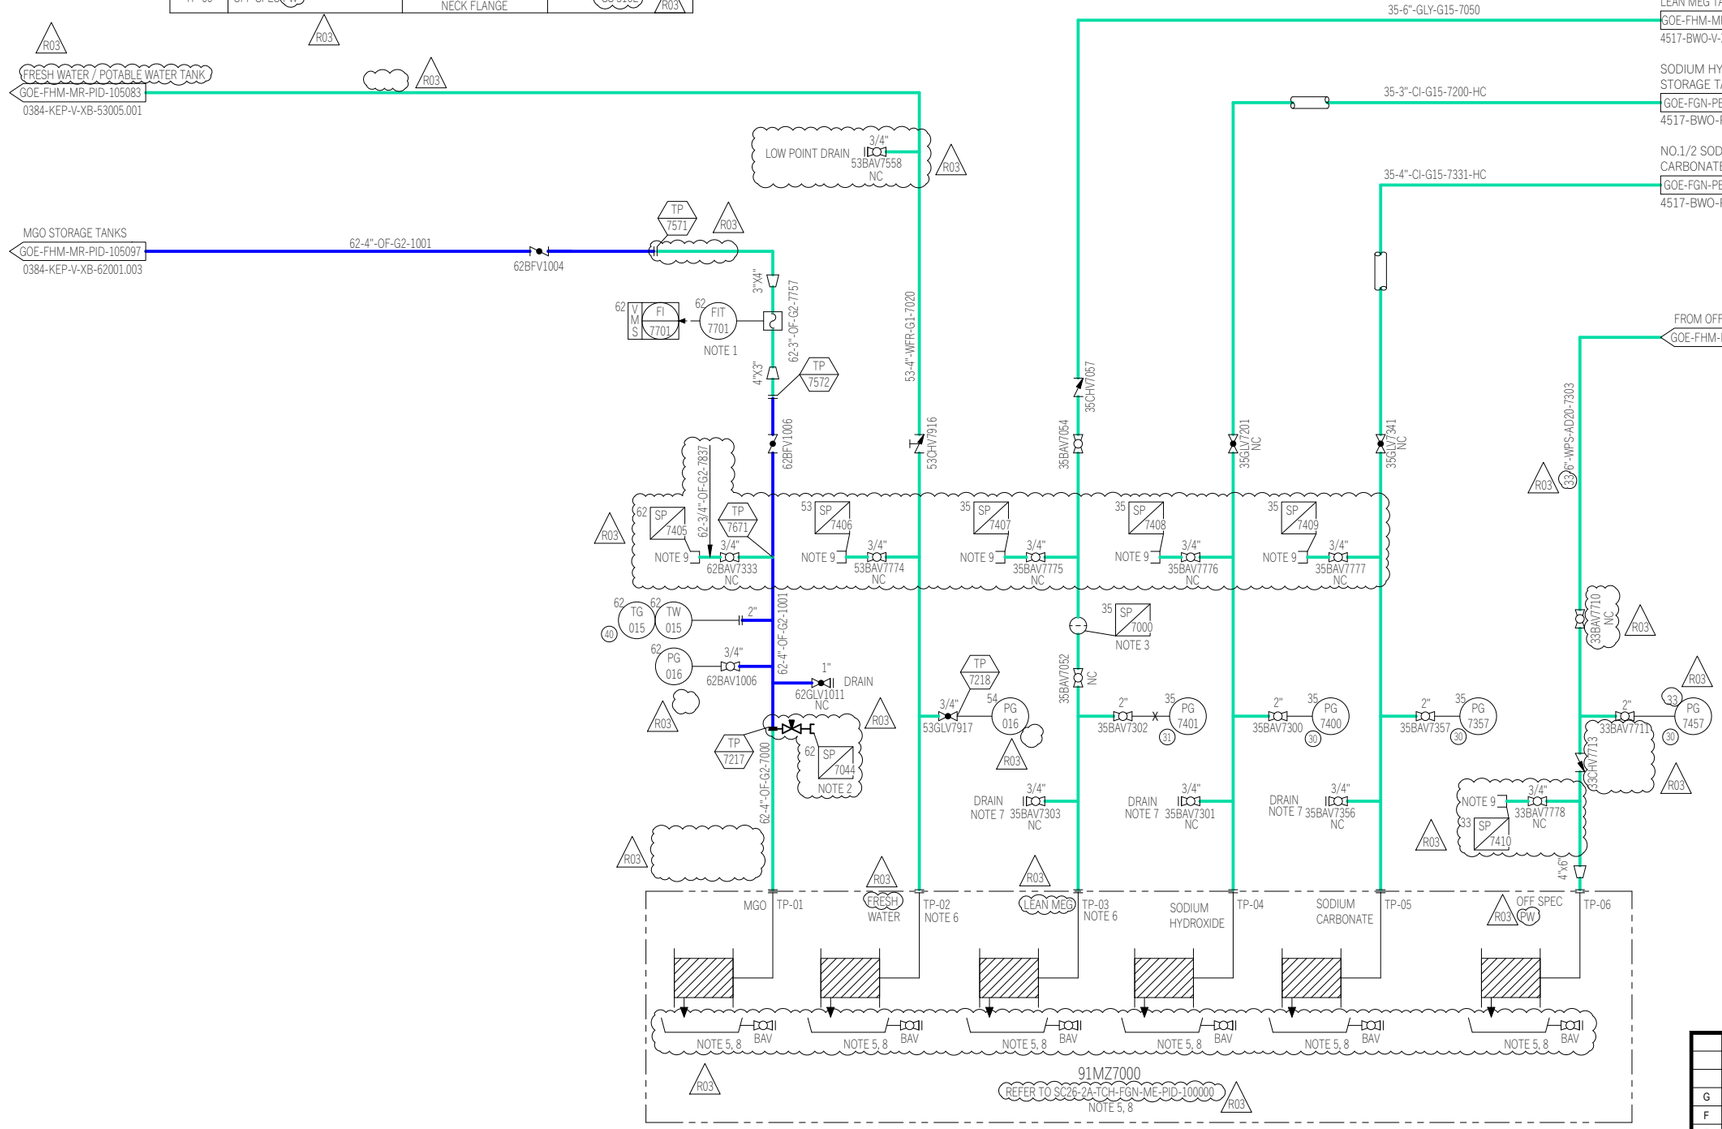

R03

SYSTEM PARAMETERS						
SERVICE	MGO	FRESH WATER	LEAN MEG	SODIUM HYDROXIDE	SODIUM CARBONATE	OFF-SPEC PW
DESIGN PRESSURE(Barg)	10	10	10	10	10	8.6
OPERATING PRESSURE(Barg)	4	4	HOLD 7	HOLD 7	HOLD 7	4-7
DESIGN TEMPERATURE(°C)	50	50	50	50	50	50
OPERATING TEMPERATURE,(°C)	AMB	AMB	AMB	AMB	AMB	40

G	R03	APPROVED FOR CONSTRUCTION	17/04/26	ZYL	DWJ	DC	SJL
F	R02	APPROVED FOR CONSTRUCTION	25/08/25	ZYL	DWJ	DC	SJL
E	R01	APPROVED FOR CONSTRUCTION	27/04/25	ZYL	DWJ	DC	SJL
D	R00	APPROVED FOR CONSTRUCTION (1st GOE ISSUE)	11/12/24	ZYL	DWJ	DC	SJL
C	R01	ISSUED FOR DESIGN / ISSUED FOR APPROVAL	10/06/24	LCE	GYSH	CHS1	HJM
B	R00	ISSUED FOR REVIEW	25/03/24	LCE	CHS1	YOLE	HJM
A	-	INTER DISCIPLINE CHECK	12/01/24	LCE	OLLI	CHS1	CHS1
GOE REV.	OTC REV.	REASON FOR USE	DATE	DRAWN	ISSUED	CHECKED	APPROVED

DISCIPLINE:	SYSTEM NO:	AREA / MODULE:	IMO NO:	PROJECT NO:	SCALE:	SIZE:
MR	62	FHM	8706014	SC26-2A	N.T.S.	A3

SUPPLIER: OceanSTAR Elite; GLOBAL OFFSHORE ENGINEERING

PROJECT: Sakarya Gas Field Dev't Phase-2a

TITLE: MARINE SYSTEM 62 - P&ID BUNKERING HOSE REEL

CLIENT: TP OTC OFFSHORE TECHNOLOGY CENTER

		GOE REV.	SHEET
OTC DOC. NO:	SC26-2A-GOE-FHM-MR-PID-105038	G	1 of 1
LEG DOC. NO:	SC26-2A-BWO-FHM-MR-PID-105038	OTC REV.	
REF. DOC. NO:	4517-BWO-V-XB-62001.001	R03	

This drawing contains proprietary information and may not be transferred, reproduced or used to construct any project other than it was issued for without the written consent of GOE or their Client.