

A

B

C

D

E

F

A

B

C

D

E

F

SYSTEM PARAMETERS		
SERVICE	MGO FOR BOILERS	FUEL GAS
DESIGN PRESSURE(Barg)	32	10
OPERATING PRESSURE(Barg)	24	5
DESIGN TEMPERATURE(°C)	60	70
OPERATING TEMPERATURE(°C)	40	35



GENERAL NOTES:

- THIS P&ID IS REISSUED FOR NECESSARY UPDATE FOR SAKARYA PROJECT.
- SEQUENTIAL NUMBER 7XXX MEANS THERE IS A MODIFICATION FROM EXISTING UNIT OR NEW.
- FOR P&ID LEGEND SHEET SEE DRAWING:
SC26-2A-GOE-FHM-MR-PID-105133 TO 105139
- FOR MARINE PIPING AND VALVE MATERIAL SPECIFICATION, SEE DOCUMENT:
SC26-2A-GOE-FHM-EP-SPC-105001 (4517-BWO-L-SA-00002)
- FOR CHANGES IN REV03, PLEASE REFER TO ECN-00310, ECN-00437




NOTES:

- DELETED.

LEGENDS:

- EXISTING PIPE
- NEW PIPE
- LIKE TO LIKE REPLACEMENT PIPE

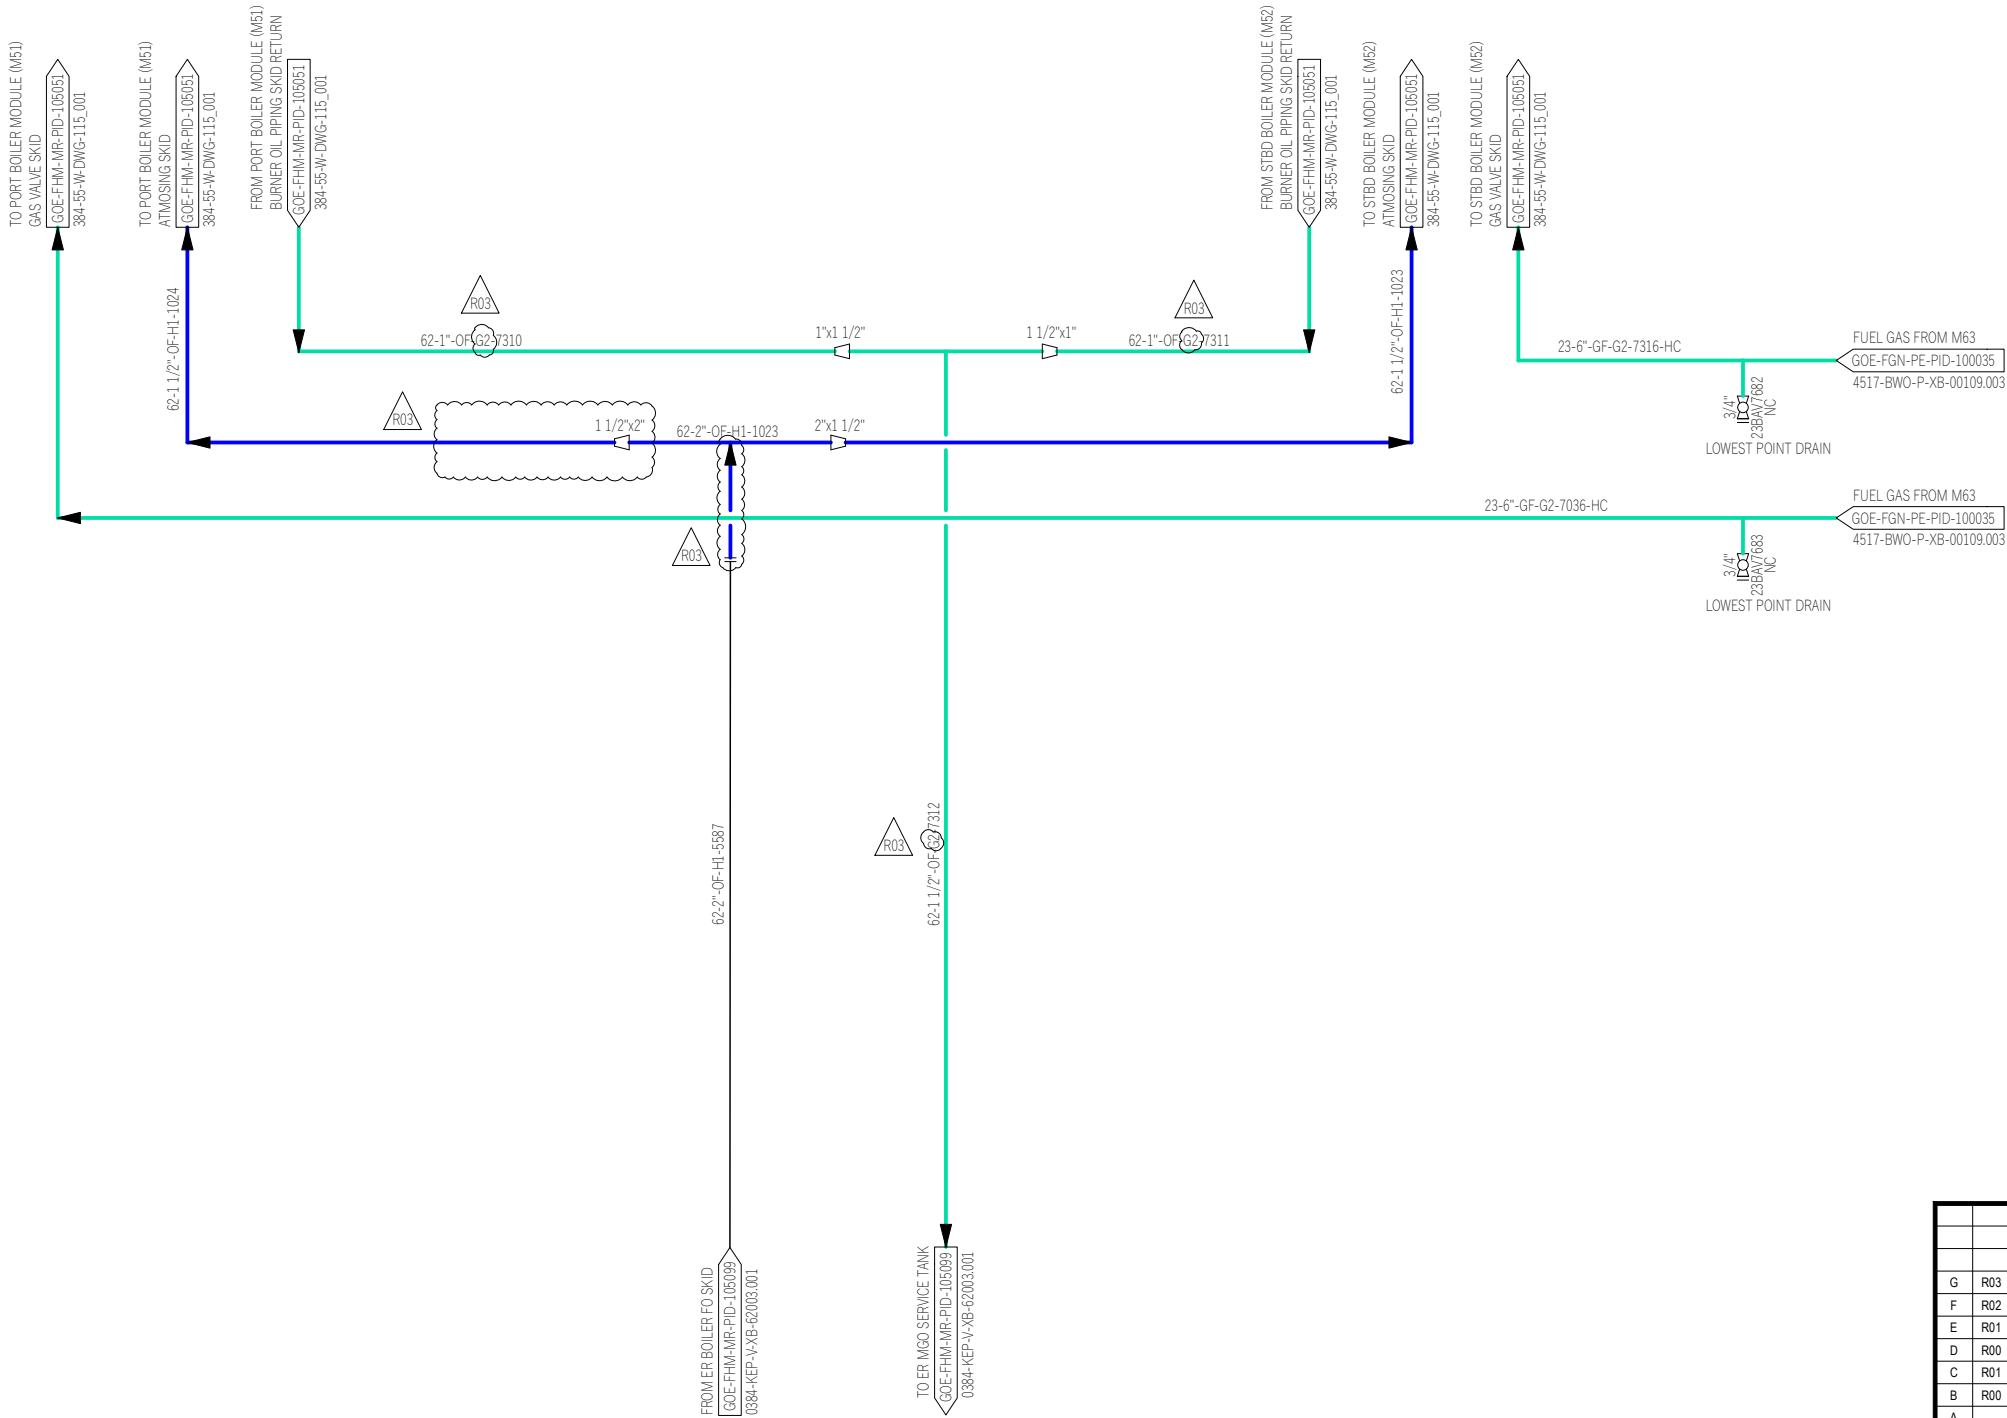

G	R03	APPROVED FOR CONSTRUCTION		20/04/26	ZYL	DWJ	DC	SJL	
F	R02	APPROVED FOR CONSTRUCTION		26/08/25	ZYL	DWJ	DC	SJL	
E	R01	APPROVED FOR CONSTRUCTION		14/05/25	ZYL	DWJ	DC	SJL	
D	R00	APPROVED FOR CONSTRUCTION(1 st GOE ISSUE)		03/12/24	ZYL	DWJ	DC	SJL	
C	R01	ISSUED FOR DESIGN / ISSUED FOR APPROVAL		25/06/24	LCE	CHS1	GYSH	HJM	
B	R00	ISSUED FOR REVIEW		14/03/24	LCE	CHS1	YOLE	HJM	
A	-	INTER DISCIPLINE CHECK		18/01/24	LCE	CHS1	OLLI	CHS1	
GOE REV.	OTC REV.	REASON FOR USE			DATE	DRAWN	ISSUED	CHECKED	APPROVED
DISCIPLINE:	SYSTEM NO.	AREA / MODULE:	IMO NO.	PROJECT NO.	SCALE:		SIZE:		
MR	62	FHM	8706014	SC26-2A	N.T.S.		A3		
SUPPLIER:		PROJECT: Sakarya Gas Field Dev't Phase-2a							
 OceanSTAR Elite		 GLOBAL OFFSHORE ENGINEERING		TITLE: P&ID - BOILER F.O. SERVICE SYSTEM					
CLIENT:		OTC OFFSHORE TECHNOLOGY CENTER				OTC DOC. NO. SC26-2A-GOE-FHM-MR-PID-105052		GOE REV. G	SHEET
 OTC						LEG DOC. NO. SC26-2A-BWO-FHM-MR-PID-105052		OTC REV. R03	1 of 1
						REF DOC. NO. 384-62-P-DWG-104_002			
This drawing contains proprietary information and may not be transferred, reproduced or used to construct any project other than it was issued for without the written consent of GOE or their Client.									