


EQUIP. TAG	71S25505-PA01	
EQUIP. NAME	WATER MIST PUMP	
CAPACITY	6.2 M3/HR	
CONFIGURATION	1 X 100%	
OPERATING (DESIGN) PRESSURE	15 (19.8)	BARG
DUTY POWER	4.35	kW

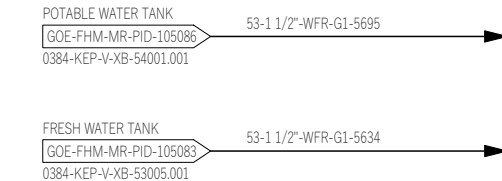

1. THIS P&ID IS REISSUED FOR INFORMATION FOR SAKARYA PROJECT.
2. NO CHANGE IN SYSTEM.
3. FOR P&ID LEGEND SHEET SEE DRAWING:
SC26-2A-GOE-FHM-MR-PID-105133 TO 105139.
4. FOR MARINE PIPING AND VALVE MATERIAL SPECIFICATION, SEE DOCUMENT:
SC26-2A-GOE-FHM-FP-SP-105001 (4517-BWO-1-SA-00002).
5. FOR CHANGES IN REV03, PLEASE REFER TO EON-00415.

-  ALARM BELL WITH LAMP
-  MANUAL RELEASE BUTTON LOCAL PROTECTION
-  FLAME DETECTOR
-  SMOKE DETECTOR

SYSTEM PARAMETERS	
SERVICE	WATER MIST
DESIGN PRESSURE(Barg)	19.8
OPERATING PRESSURE(Barg)	15
DESIGN TEMPERATURE(°C)	50
OPERATING TEMPERATURE(°C)	32

_____ EXISTING PIPE

-	R03	ISSUED FOR INFORMATION		08/05/26	ZYL	DWJ	DC	SJL
-	R02	ISSUED FOR INFORMATION		04/09/25	ZYL	DWJ	DC	SJL
-	R01	ISSUED FOR INFORMATION		14/05/25	ZYL	DWJ	DC	SJL
-	R00	ISSUED FOR INFORMATION (1 st GOE ISSUE)		15/01/25	ZYL	DWJ	DC	SJL
Z0	-	ISSUED FOR AS-BUILT		28/09/22	JT	JT	NO	PL
02	-	RE-ISSUED FOR CONSTRUCTION		07/04/21	XH	JT	NO	PL
01	-	RE-ISSUED FOR CONSTRUCTION		08/09/20	XH	JT	NO	PL
00	-	ISSUED FOR CONSTRUCTION		23/12/19	XH	JT	NO	PL
C	-	ISSUED FOR DESIGN		12/09/19	XH	JT	NO	PL
B	-	ISSUED FOR REVIEW		15/08/19	XH	JT	NO	PL
A	-	ISSUED FOR IDC		09/07/19	XH	JT	NO	PL
GOE REV.	OTC REV.	REASON FOR USE		DATE	DRAWN	ISSUED	CHECKED	APPROVED
DISCIPLINE: MR	SYSTEM NO: 71	AREA / MODULE: FHM	MO NO: 8706014	PROJECT NO: SC26-2A	SCALE: N.T.S.	SIZE: A3		
SUPPLIER:  OceanSTAR Elite			PROJECT: Sakarya Gas Field Dev't Phase-2a					
CLIENT:  OTC OFFSHORE TECHNOLOGY CENTER			TITLE: P&ID - LOCAL APPLICATION WATER MIST SYSTEM IN ENGINE ROOM					
			OTC DOC. NO: SC26-2A-GOE-FHM-MR-PID-105118				GOE REV. -	SHEET 1 of 1
			LEG DOC. NO: -				OTC REV. R03	
			REF DOC. NO: 0348-KEP-V-XB-71006.001					
This drawing contains proprietary information and may not be transferred, reproduced or used to construct any project other than it was issued for without the written consent of GOE or their Client.								