


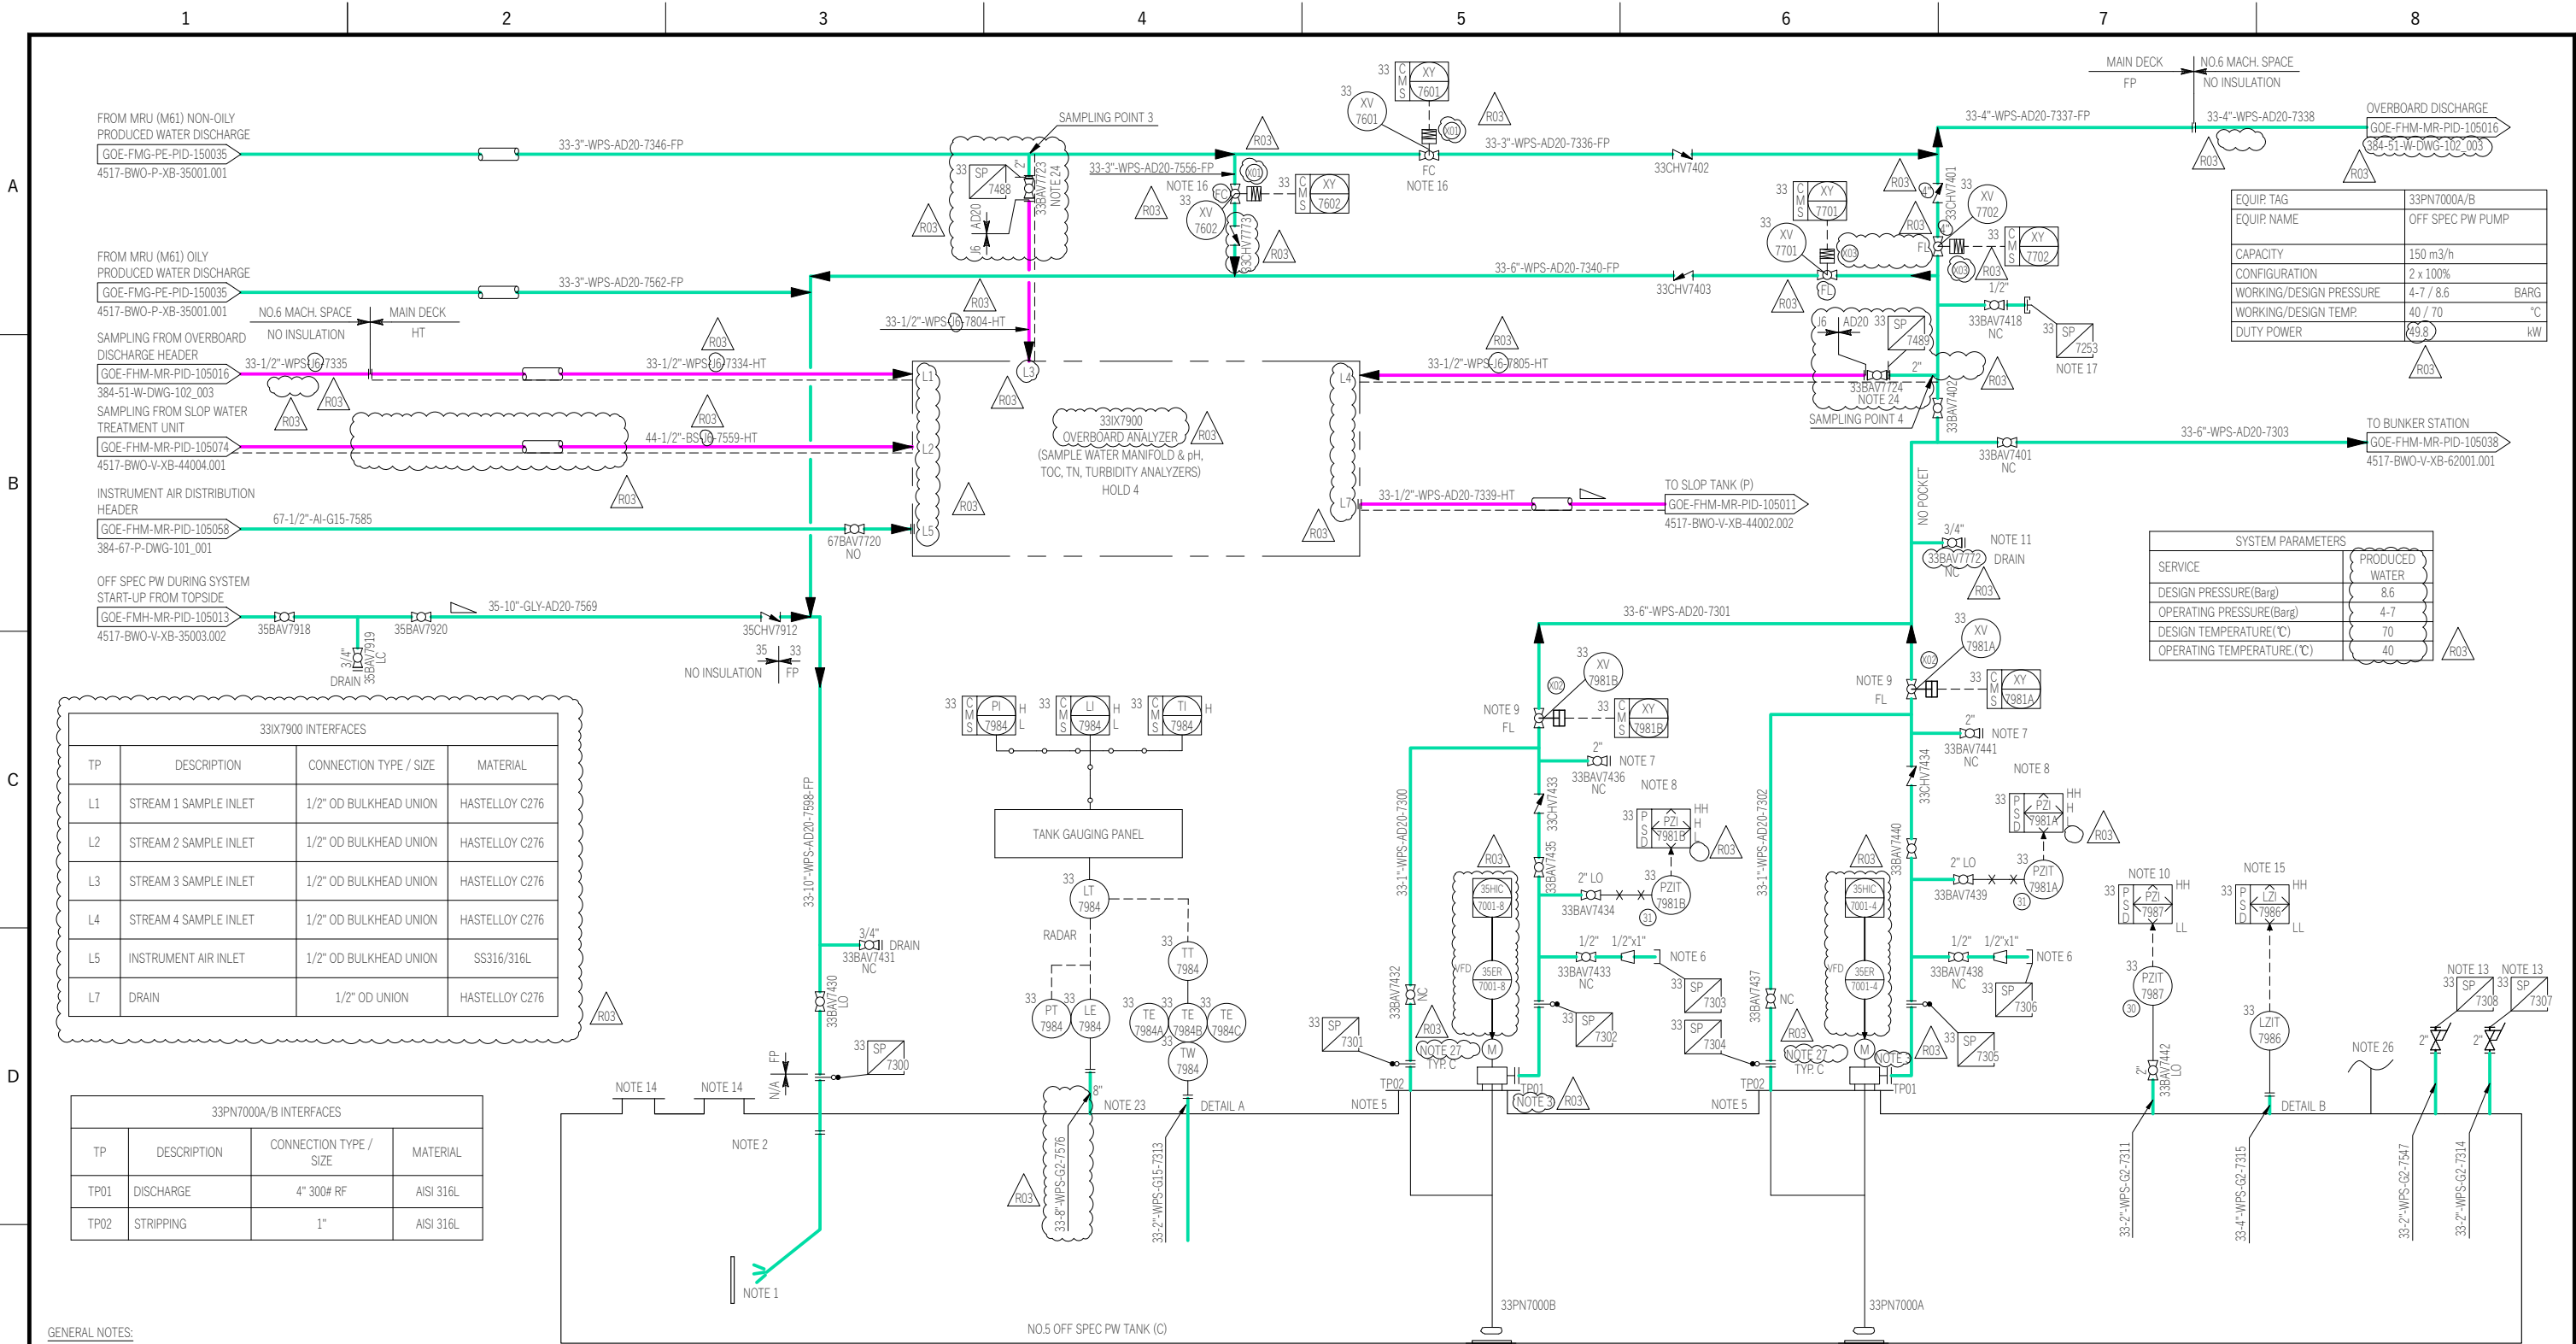

GENERAL NOTES:

- FOR P&ID LEGEND SHEET SEE DRAWING: SC26-2A-GOE-FHM-MR-PID-105133 TO 105139.
- FOR MARINE PIPING AND VALVE MATERIAL SPECIFICATION, SEE DOCUMENT: SC26-2A-GOE-FHM-EP-SPC-105001(4517-BWO-L-SA-00002).
- FOR CHANGES IN REV03, PLEASE REFER TO ECN-00318, ECN-00472.

HOLDS:

- DELETED.
- DELETED.
- DELETED.
- SAMPLE SYSTEM PROCESS DATA TO BE CONFIRMED.
- DELETED.
- DELETED.
- DELETED.
- DELETED.
- DELETED.


LEGENDS:

- NEW PIPE
- SAMPLING PIPE
- HEAT TRACED PIPE
- SAMPLE QUILL

NOTES:

- TANK LOADING PIPE END TO BE 5M ABOVE TANK BOTTOM.
- TANK INLET PIPE (BENEATH DECK PENETRATION) SHALL BE PROVIDED WITH VENT HOLES (ø25MM x 2EA) TO PREVENT SIPHONIC EFFECT AND ALLOW GAS FREEING OF DROP LINE.
- COUNTER-FLANGE TO BE PROVIDED BY PUMP VENDOR.
- DELETED.
- PUMP MANUFACTURER'S DECK TRUCK.
- N2 INLET CONNECTION FOR STRIPPING OPERATION.
- FLEXIBLE HOSE TO BE CONNECTED TO PUMP DRAIN HEADER FOR EMPTYING THE TANK IN CASE OF LIQUID CONTAMINATION ETC.
- PRESSURE ALARM HIGH-HIGH TO STOP PUMP.
- DISCHARGE VALVE TO BE INTERLOCKED AND CLOSED BY CMS WHEN PUMP IS NOT RUNNING.
- TANK PRESSURE LOW LOW ALARM TO STOP PUMP IN TANK. TANK PRESSURE HIGH HIGH ALARM TO CLOSE LOADING VALVE MANUALLY.
- DRAIN VALVE TO BE LOCATED AT THE LOWEST POINT OF THE OFFLOADING LINE. TO DRAIN THE ACCUMULATED LIQUID INSIDE PIPE IN COLD WEATHER TO PREVENT FREEZING.
- DELETED.
- VAPOUR LOCK VALVE FOR SOUNDING / SAMPLING.
- EXISTING HATCH FOR POTABLE TANK CLEANING MACHINE.
- TANK LEVEL HIGH HIGH ALARM TO STOP PRODUCED WATER DISCHARGE FROM TOPSIDE. TANK LEVEL LOW LOW ALARM TO TRIP PUMP 33PN7000A/B.
- PRODUCED WATER FROM MRU TO BE DISCHARGED OVERBOARD UNLESS ANY OF THE ANALYSIS RESULTS IS OUT AS WELL AS WHEN SEAWATER OVERBOARD IS OUT OF SERVICE.
- CHEMICAL INJECTION VIA 1/2" TODO COUPLING.
- DELETED.
- DELETED.
- SENSOR TO BE PROVIDED WITH SUBSTANCE CONTENT HIGH LEVEL ALARM.
- DELETED.
- DELETED.
- NEW 8" PENETRATION SPOOL TO BE PROVIDED BY EMERSON.
- VALVE TO BE PLACED NEAR TO THE MAIN PIPE. 2" 150# RF FLANGE W/ 1/2" NPTM x 1/2" OD SDSS TUBING ADAPTOR TO BE PROVIDED BY EMERSON.
- RADAR BEAM CLEARANCE IN VESSEL BOTTOM OF ø4.3 M IS REQUIRED FOR LZIT.
- FOR N2 SUPPLY & VENT, PVV BREATHING AND AERATION ARRANGEMENT, REFER TO P&ID SC26-2A-GOE-FHM-MR-PID-105061 (384-91-P-DWG-100\_002), SC26-2A-GOE-FHM-MR-PID-105062 (384-91-P-DWG-100\_003).
- A SOFTWARE HIC (HAND INDICATING CONTROLLER) IN CCR TO BE PROVIDED TO ALLOW THE OPERATOR TO REGULATE PUMP SPEED.

DETAIL A  
TEMPERATURE TRANSMITTER

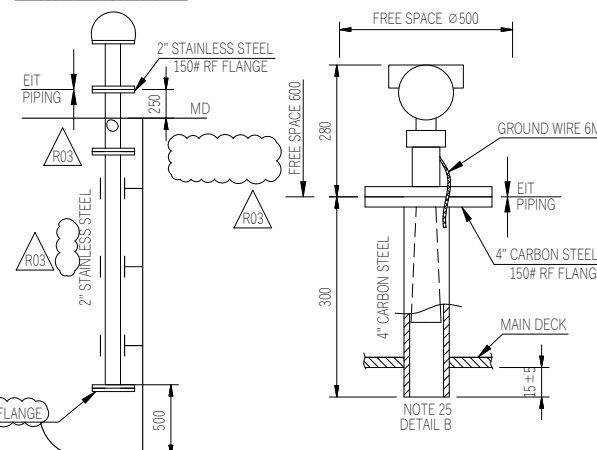

|   |            |                           |                |                                           |             |        |                               |         |                 |                     |
|---|------------|---------------------------|----------------|-------------------------------------------|-------------|--------|-------------------------------|---------|-----------------|---------------------|
|   |            |                           |                |                                           |             |        |                               |         |                 |                     |
| E   | R03        | APPROVED FOR CONSTRUCTION |                |                                           | 28/04/26    | ZYL    | DWJ                           | DC      | SJL             |                     |
| D   | R02        | APPROVED FOR CONSTRUCTION |                |                                           | 07/11/25    | ZYL    | DWJ                           | DC      | SJL             |                     |
| C   | R01        | ISSUED FOR APPROVAL       |                |                                           | 17/09/25    | ZYL    | DWJ                           | DC      | SJL             |                     |
| B   | R00        | ISSUED FOR REVIEW         |                |                                           | 11/07/25    | ZYL    | DWJ                           | DC      | SJL             |                     |
| A   | -          | INTER-DISCIPLINE CHECK    |                |                                           | 30/04/25    | ZYL    | DWJ                           | DC      | SJL             |                     |
| GOE<br>REV   | OTC<br>REV | REASON FOR USE            |                |                                           | DATE        | DRAWN  | ISSUED                        | CHECKED | APPROVED        |                     |
| DISCIPLINE:   |            | SYSTEM NO:                | AREA / MODULE: | IMO NO:                                   | PROJECT NO: | SCALE: | SIZE:                         |         |                 |                     |
| MR   |            | 33                        | FHM            | 8706014                                   | SC26-2A     | N.T.S. | A3                            |         |                 |                     |
| SUPPLIER:   |            |                           |                | PROJECT: Sakarya Gas Field Dev't Phase-2a |             |        |                               |         |                 |                     |
| <br>OceanSTAR Elite                                                                                               |            |                           |                | TITLE:                                    |             |        |                               |         |                 |                     |
|   |            |                           |                | P&ID - OFF SPEC PRODUCED WATER TANK (C)   |             |        |                               |         |                 |                     |
| CLIENT:   |            |                           |                | OTC DOC. NO:                              |             |        | SC26-2A-GOE-FHM-MR-PID-105128 |         | GOE REV:<br>E   | SHEET<br><br>1 of 1 |
|  OFFSHORE<br>TECHNOLOGY<br>CENTER                                                                                 |            |                           |                | LEG DOC. NO:                              |             |        | -                             |         | OTC REV:<br>R03 |                     |
|   |            |                           |                | REF DOC. NO:                              |             |        | -                             |         |                 |                     |
| This drawing contains proprietary information and may not be transferred, reproduced or used to construct any project other than it was issued for without the written consent of GOE or their Client. |            |                           |                |                                           |             |        |                               |         |                 |                     |

This drawing contains proprietary information and may not be transferred, reproduced or used to construct any project other than it was issued for without the written consent of GOE or their Client.